



REPUBLIKA E KOSOVËS / REPUBLIKA KOSOVA / REPUBLIC OF KOSOVO

QEVERIA E KOSOVËS / VLADA KOSOVA / GOVERNMENT OF KOSOVA

MINISTRIA E EKONOMISË DHE AMBIENTIT / MINISTARSTVO EKONOMIJE I ŽIVOTNE SREDINE / MINISTRY OF ECONOMY AND ENVIRONMENT


AGJENCIA KADASTRALE E KOSOVËS / KATASTARSKA AGENCIJA KOSOVA / KOSOVA CADASTRAL AGENCY

Raport i njësisë kadastrale

Zonë kadastrale: Greme

Lloji i njësisë kadastrale: Parcelë

Nr i njësisë kadastrale: P-72217024-02171-0

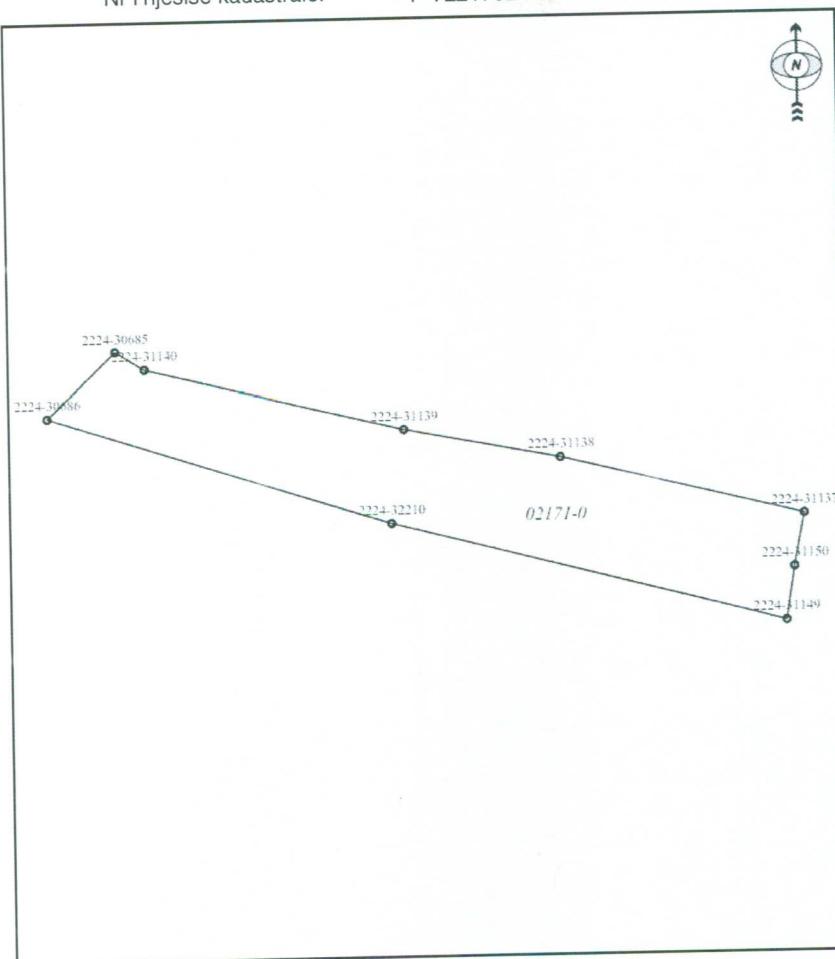

Pika	Y	X
2224-31149	7512383.216	4687377.302
2224-32210	7512310.047	4687396.423
2224-30686	7512245.989	4687417.244
2224-30685	7512258.843	4687429.217
2224-31140	7512264.278	4687425.894
2224-31139	7512312.558	4687414.070
2224-31138	7512341.557	4687408.422
2224-31137	7512386.736	4687397.151
2224-31150	7512384.816	4687387.241

Sip.Graf. 2432 m²

Scale: 1:1290

Krijuar nga

Pozita:

Emri:

Mbiemri:

Emri i shfrytëzuesit(kodi):

Data

Koha:

Nenshkrimi:





REPUBLIKA E KOSOVËS / REPUBLIKA KOSOVA / REPUBLIC OF KOSOVO

QEVERIA E KOSOVËS / VLADA KOSOVA / GOVERNMENT OF KOSOVA

MINISTRIA E EKONOMISË DHE AMBIENTIT / MINISTARSTVO EKONOMIJE I ŽIVOTNE SREDINE / MINISTRY OF ECONOMY AND ENVIRONMENT


AGJENCIA KADASTRALE E KOSOVËS / KATASTARSKA AGENCIJA KOSOVA / KOSOVA CADASTRAL AGENCY

Raport i njësisë kadastrale

Zonë kadastrale: Greme

Lloji i njësisë kadastrale: Parcelë

Nr i njësisë kadastrale: P-72217024-02172-0

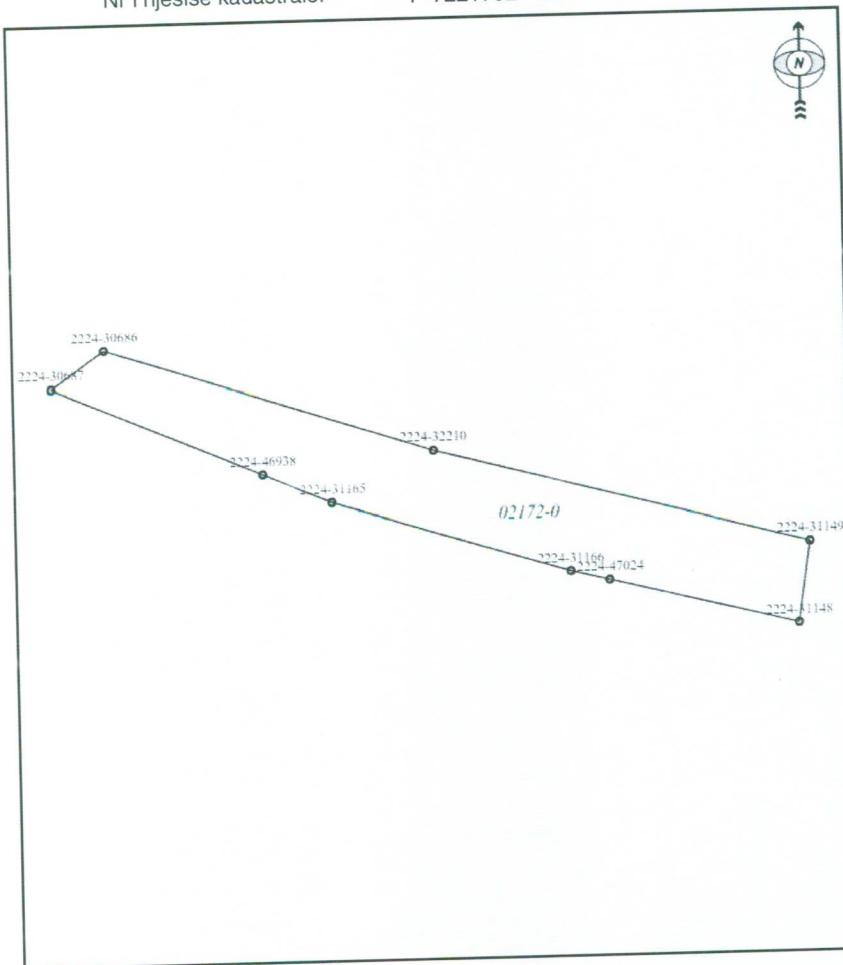

Pika	Y	X
2224-31148	7512380.816	4687361.202
2224-47024	7512343.958	4687370.528
2224-31166	7512336.426	4687372.433
2224-31165	7512289.957	4687386.834
2224-46938	7512276.575	4687392.517
2224-30687	7512235.519	4687409.955
2224-30686	7512245.989	4687417.244
2224-32210	7512310.047	4687396.423
2224-31149	7512383.216	4687377.302

Sip.Graf.2199 m²

Scale: 1:1354

Krijuar nga

Pozita:

Emri:

Violeta

Mbiemri:

Aliu

Emri i shfrytëzuesit(kodi):

Violeta.Aliu

Data

30.10.2020

Koha:

08:40:50

Nenshkrimi:





REPUBLIKA E KOSOVËS / REPUBLIKA KOSOVA / REPUBLIC OF KOSOVO


QEVERTA E KOSOVËS / VLADA KOSOVA / GOVERNMENT OF KOSOVA

MINISTRIA E EKONOMISË DHE AMBIENTIT / MINISTARSTVO EKONOMIJE I ŽIVOTNE SREDINE / MINISTRY OF ECONOMY AND ENVIRONMENT

AGJENCIA KADASTRALE E KOSOVËS / KATASTARSKA AGENCIJA KOSOVA / KOSOVA CADASTRAL AGENCY

Raport i njësisë kadastrale

Zonë kadastrale: Greme
Lloji i njësisë kadastrale: Parcelë
Nr i njësisë kadastrale: P-72217024-02173-1

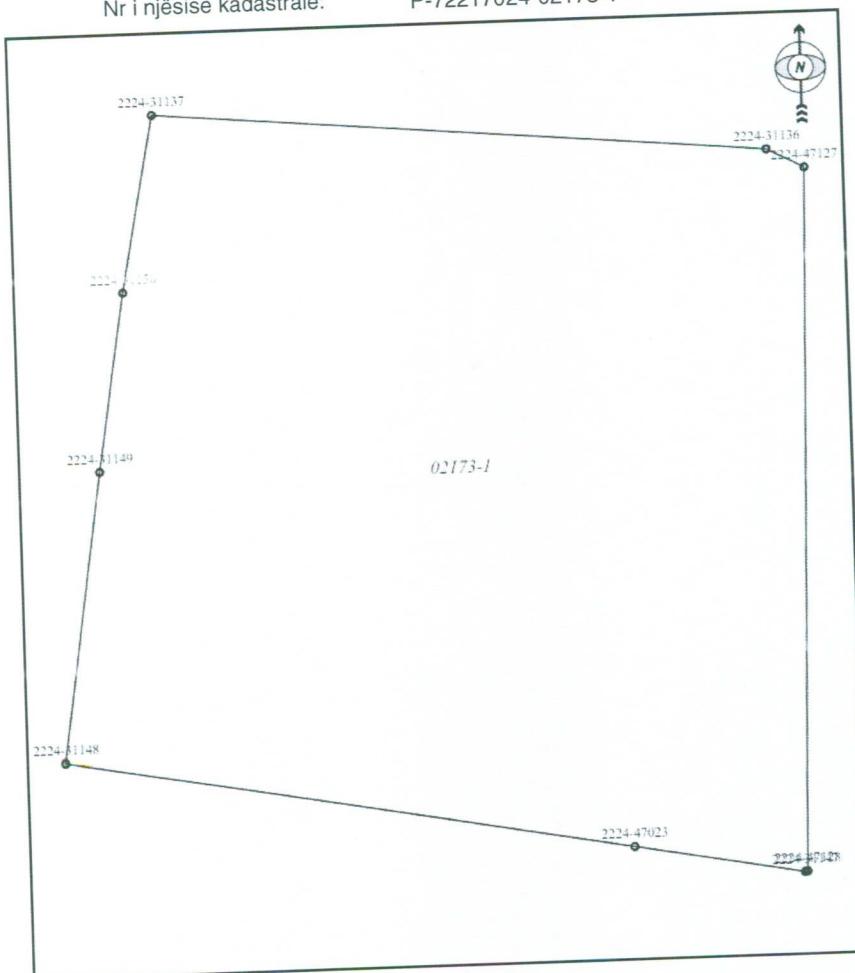

Pika	Y	X
2224-47127	7512423.087	4687392.984
2224-47128	7512422.066	4687353.816
2224-31147	7512421.925	4687353.781
2224-47023	7512412.443	4687355.493
2224-31148	7512380.816	4687361.202
2224-31149	7512383.216	4687377.302
2224-31150	7512384.816	4687387.241
2224-31137	7512386.736	4687397.151
2224-31136	7512420.995	4687394.070

Sip.Graf.1500 m²

Scale: 1:387

Krijuar nga

Pozita:

Emri: Violeta

Mbiemri: Aliu

Emri i shfrytëzuesit(kodi):
Violeta.Aliu

Data: 30.10.2020

Koha: 08:42:34

Nenshkrimi:





Numri i Protokollit

238/2020

**Republika e Kosovës
Republika Kosova-Republic of Kosovo
Qeveria -Vlada-Government**

Ministria e Mjedisit dhe Planifikimit Hapësinor /Ministarstvo Sredine i Prostornog Planiranja/Ministry of Environment and Spatial Planning
AGJENCIJA KADASTRALE E KOSOVËS / KATASTARSKA AGECA KOSOVA / KOSOVA CADASTRAL AGENCY

Formulari nr. 5

KËRKESË PËR SHERBIMET KADASTRALE NGA GJEODETI APO KOMPANIJA GJEODETE E LICENCUAR

Gjeodeti Kompania gjeodete e licencuar: Sead Prushi

Numri i licencës: 152

Komuna: Ferizaj

Zona Kadsatrale: GREME

Numri i njësisë kadastrale: 2171-0.2172-0.2173-1

1. Të dhënat për parashtruesin e kërkesës

Emri / Emri i Kompanisë: Tahir

Mbiemri: Shehu

Emri i prindit: Rexhep

Numri personal: 1006181216

Adresa: Fsh. Greme- Ferizaj

Numri i biznesit: (për person juridik dhe kompani)

Nr. Tel: +383 44/496-873

2. Parashtruesi i kërkesës: Pronar - Shfrytëzues - Përfaqësues i Autorizuar**3. Lista e dokumenteve të nevojshme:**

Pronari/Shfrytëzuesi	Përfaqësues i Autorizuar
1 <input type="checkbox"/> Letërnjoftimin / Certifikatë biznesi (kopje)	1 <input type="checkbox"/> Letërnjoftimin / Certifikatë biznesi (kopje)
2 <input checked="" type="checkbox"/> Vërtetimi i tatimit në pronë	2 <input type="checkbox"/> Vërtetimi i tatimit në pronë
3 <input type="checkbox"/> Çertifikata e pronës	3 <input type="checkbox"/> Çertifikata e pronës
4 <input type="checkbox"/> Kopja e planit	4 <input type="checkbox"/> Kopja e planit

4. Kërkesa për:

1 <input type="checkbox"/> Ndërrim të kulturës së parcelës	6 <input type="checkbox"/> Matjen dhe regjistrimin e ndërtesës
2 <input type="checkbox"/> Ndarjen e parcelës	7 <input type="checkbox"/> Matjen dhe regjistrimin e pjesës së ndërtesës
3 <input checked="" type="checkbox"/> Bashkimin e parcelës	8 <input type="checkbox"/> Punë të veçanta gjeodezike
4 <input type="checkbox"/> Përaktimin e kufijve të parcelës	9 <input type="checkbox"/> Matja e ndërtesës për legalizim
5 <input type="checkbox"/> Ri-regullimin e kufirit të parcelës	10 <input type="checkbox"/> Riregjistrim i pjesës grafike

Data: 28.10.2020



Nënshkrimi: _____



REPUBLIKA E KOSOVËS - REPUBLIKA KOSOVA - REPUBLIC OF KOSOVA
KOMUNA FERIZAJ - OPŠTINA UROŠEVAC - MUNICIPALITY OF FERIZAJ
DREJTORIA E PRONËS, KADASTRIT DHE GJEODEZISË



FATURE-RACUN-INVOICE

NF/FN/NB600629804

Nr. Serik/Ser Brj/Ser No
2520002861

Emri/Mbiemri Ilme/Prezime Name/Surname	Sead Prushi	
Pershkrimi Opis Description	10-942/05-0093269/20 - Kerkese per blerjen e produkteve kadastrale, parc.nr.2171-0,2172-0,2173-1 ZK G	
Shuma Iznos Amount	20.00	Data Datum Date
Llogaria Bankare Broj Zitoracuna Bank Account	1000650030000035	
Leshuar nga Izdalo od Issued by	Fitnate.Bajrami	



30 OCT 2020
Arka 28 Ferizaj

Nenshkrimi dhe vuja e bankes
Potpis i peçat banke
Bank signature and stamp



FEG9D2520002861J

I.F.J.B. VLLESA-CO

FLETËPAGESË

VL00281604043064
028 FERIZAJ - F. BISLIMI

30.10.2020
08:31

SHUMA:

20.00 €

PROVIZIONI:

0.80 €

TOTALI:

20.80 €

Llogaria: KOMUNA FERIZAJ

Nr. llogarisë: 1000650030000035



PAGUESI:

SEAD PRUSHI

NR.SERIK:

2520002861

PERSHKRIMI:

KERKESE PER BLERJEN

UNIREF:

FEG9D2520002861J



Nënshkrimi i paguesit

Nënshkrimi i arkëtarit



Matje Gjeodezike
Shërbime Kadastrale
Projektive Inxhinierike
Tel: +383 (0) 49-535-250
liridonsejdiu88@gmail.com

N.SH."Geo Coding"

Faturē

Nr: 68/2020

Shitësi:

N.SH."Goe Coding"

Blerësi:

Tahir (Rexhep) Shehu

Pronari:

LIRIDON SEJDIU

Nr. ID:

1006181216

NBB-

811384528

NRB.

Numri Fiskal:

811384528

Nr. Fiskal

Adresa

Rr. "12 Qershori" - Ferizaj

Adresa

II / Bankare

130400100278326000.00%

Data: 11/02/2020

Pagesa: Permes banks

Komenti: 1. BPB 13-04-0010027832.69
2. Banka Ekonomike 1304001002783269

Pranoti



Dorézai:



Republika e Kosovës

Republika Kosova - Republic of Kosovo

Qeveria e Kosovës - Vlada Kosova - Government of Kosovo

Ministria e Infrastrukturës dhe Ambientit/ Ministrastvo Infrastrukture i Sredine/ Ministry of Infrastructure and Environment

AGJENCIA KADASTRALE E KOSOVËS/ KOSOVSKA KATASTARSKA AGENCIJA/ KOSOVA CADASTRAL AGENCY

MBËSHTJELLËS I LËNDËS

Gjeodeti / Kompania gjeodete e licencuar: **SEAD PRUSHI**

Numri i licencës: **152**

Numri i Protokollit: **238/2020**

LËNDA:

1. Ndërrim të kulturës së parcelës
2. Ndarjen e parcelës
3. Bashkimin e parcelës
4. Përcaktimin e kufijve të parcelës
5. Ri-rregullimin e kufirit të parcelës
6. Matjen dhe regjistrimin e ndërtesës
7. Matjen dhe regjistrimin e pjesës së ndërtesës
8. Regjistrimi i servitutit
9. Punë të veçanta gjeodezike
10. Matja e ndërtesës për legalizim

“GJEODET I LICENCUAR”

+383 44 791 828

e-mail: progeo2017@gmail.com

Data: **31/10/2020**

Vendi: **FERIZAJ**

.....

(Nënshkrimi dhe vula)

Përbajtja:

1. Kërkesa e palës
 2. Dëshmia e burimit të të dhënave zyrtare
 3. Dëshmia e pagesës për të dhënat e pranuara
 4. Fatura apo kuponi fiskal e lëshuar shërbimet kadastrale sipas UA 11/2019 dhe 12/2019
 5. Procesverbali nga terreni
 6. Manuali i njësive kadastrale
 7. Regjistri i ndërrimeve
 8. Lista e koordinatave të matura
 9. Formulari i korrigjimit të sipërfaqes
 10. Leternjoftimi i pronarit
 11. Certifikatën e pronësisë
 12. Raporti teknik
 13. Leternjoftimi kopje i fqinjëve
 14. Dokumentacioni i gjeodetit të licencuar

Dokumente tjerar:

REPUBLIKA E KOSOVËS
REPUBLIKA KOSOVO

REPUBLIC OF KOSOVO
ID CARD



Мялен / Презиме / Surname

SHEHU

Emri / Име / Given name

TAHIR

Datelinëja / Датум рођења / Date of birth

15.04.1937

Shtetësia / Држављанство / Nationality

KOSOVAR

Vendlindja / Место гођења / Place of birth

GREME

Gjina / Пол / Sex

M

Data e skadimit / Датум истека / Date of expiry

25.10.2028

Nënshtkimi / Потпис / Signature

Tahir Shehu

052919



Data e lëshimit / Датум издавања / Date of issue

26.10.2018

Lëshuar nga / Издан од / Issued by

MPB / MUP / MIA

Nr. Personal / Лични Бр. / Personal No

1006181216

Nr. Lnj / Бр. П.К. / ID Card No

ID1111956

Vendbanimi / Пребивалиште / Residence

GREME, FERIZAJ

1561<<<<<<<<<<<<
IDRKSID1810250RKS1006181216<2
370412TAHIR<<<<<<<<<<<<<
SH



Republika e Kosovës / Republika Kosova / Republic of
Komuna e FERIZAJ / Opština UROŠEVAC / Municipality



Bazuar në nenin 18 të ligjit 03/L-204 për tatimin në pronë, si dhe udhëzimit administrativ nr. 7/2011 të lëshuar nga MF, i cili ka të bëjë me urdhëresat e ndalimit të shërbimeve komunale për detyrim të pagesës së tatimit në Na osnovu člana 18, zakona 03/L-204 za poreza na imovinu i administrativne uredbe MF br. 7/2011, u vezi zabrane opštinskih usluga za prinudu uplate poreza na imovinu, izdaje se ova:

Based on the article 18 of LAW 03/L-204 on property tax and administrative instruction MF no. 7/2011 on termination of services for enforcement of the municipal property tax, the municipal Property Tax Office

Nr / Br / No

22523687

29/10/2020

VËRTETIM POTVRDA CERTIFICATE

Me të cilin vërtetohet se tatimpaguesi
Kojim se potvrđuje da je poreznik
that certifies that taxpayer

TAHIR SHEHU

FERIZAJ
Komuna / Opština / Municipality

FERIZAJ PN
adresa / address

I ka kryer pjesërisht / plotësisht obligimet e tatimit në pronë
Delimično/ izveršio uplatu poreskih obaveza
has partially / fulfilled obligations on property tax

TAHIR REXHEP SHEHU

Vërtetimi lëshohet në bazë të kërkesës së / Potvrda se izdaje na zahteve / Certificate is issued by

Për nevoja personale
dhe shërben për / i služi za / and is used for

Shënime shtesë / Druge podatke / Additional info





Republika e Kosovës

Republika Kosova-Republic of Kosovo

Qeveria e Kosovës- Vlada Kosova- Government of Kosovo

Ministria e Infrastrukturës dhe Ambientit/ Ministrastvo Infrastrukture i Sredine/ Ministry of Infrastructure and Environment

AGJENCIA KADASTRALE E KOSOVËS/KOSOVSKA KATASTARSKA AGENCIJA/ KOSOVO CADASTRAL AGENCY

PROCESVERBALI NGA TERRENI

Gjeodeti - Kompania gjeodete e licencuar: Sead Prushi	Numri i licencës: 152
---	-----------------------

Komuna: Ferizaj	Zona Kadastrale: Greme
-----------------	------------------------

Numri i njësisë kadastrale:	2171-0, 2172-0, 2173-1
-----------------------------	------------------------

Matja/piketimi është realizuar me:	
GPS GNSS	<input checked="" type="checkbox"/>
Stacion Total	<input type="checkbox"/>

1. Përshkimi i procesit:

DATË PËR BASHKIRIJIU E DARC. TË LARTË SHËNUAR, DHE
NDARIJEN E SAD S PAS SIPERFAQEVE TË KUSHTËZUARA
ZOARI UJERAT AVE DHE Tjetra e dibratur.

2. Vërejtje:

3. Nënshkrimi i palëve

Pronarët janë pajtuar me pikat definitive kufitare të vendosura në terren nga të cilat derivohet sipërfaqja definitive që do të regjistrohet në Sistemin e Informacioneve Kadastrale për Tokën në Kosovë.

Të poshtëshënuarve u lexohet procesverbal i dhe nëse pajtohen me atë nënshkruajnë më poshtë, në të kundërtën jepin arsyet e mospajtimit.

Emri (emri i prindit) mbiemri	Numri personal	Numri i njësisë kadastrale	Nënshkrimi
TAHIR KREXHEPI SHEHU	1006181216		Tahir Shehu

Nënshkrimi dhe vula e gjodetit



Data: 30/10/2020



Republika e Kosovës
Republika Kosova-Republic of Kosova
Qeveria - Vlada-Government

Ministria e Mjedisit dhe Planifikimit Hapësinor /Ministarstvo Sredine i Prostornog Planiranja/Ministry of Environment and Spatial Planning
AGJENCIJA KADASTRALE E KOSOVËS / KATASTARSKA AGECIJA KOSOVA/ KOSOVA CADASTRAL AGENCY

2171-0 2172-0
2173-1



Zyra kadastrale komunale / Opštinska katastarska kancelarija: Ferizaj

Zona kadastrale / Katastarska zona: Greme

Lloji i njësisë kadastrale / Vrsta katastarske jedinice : Parcelë

Nr. i njësisë kadastrale / Br. katastarske jedinice : _____
Numri i lëndës / Broj predmeta: _____

Shkalla e zvoglimit / Razmera plana : 1:1000

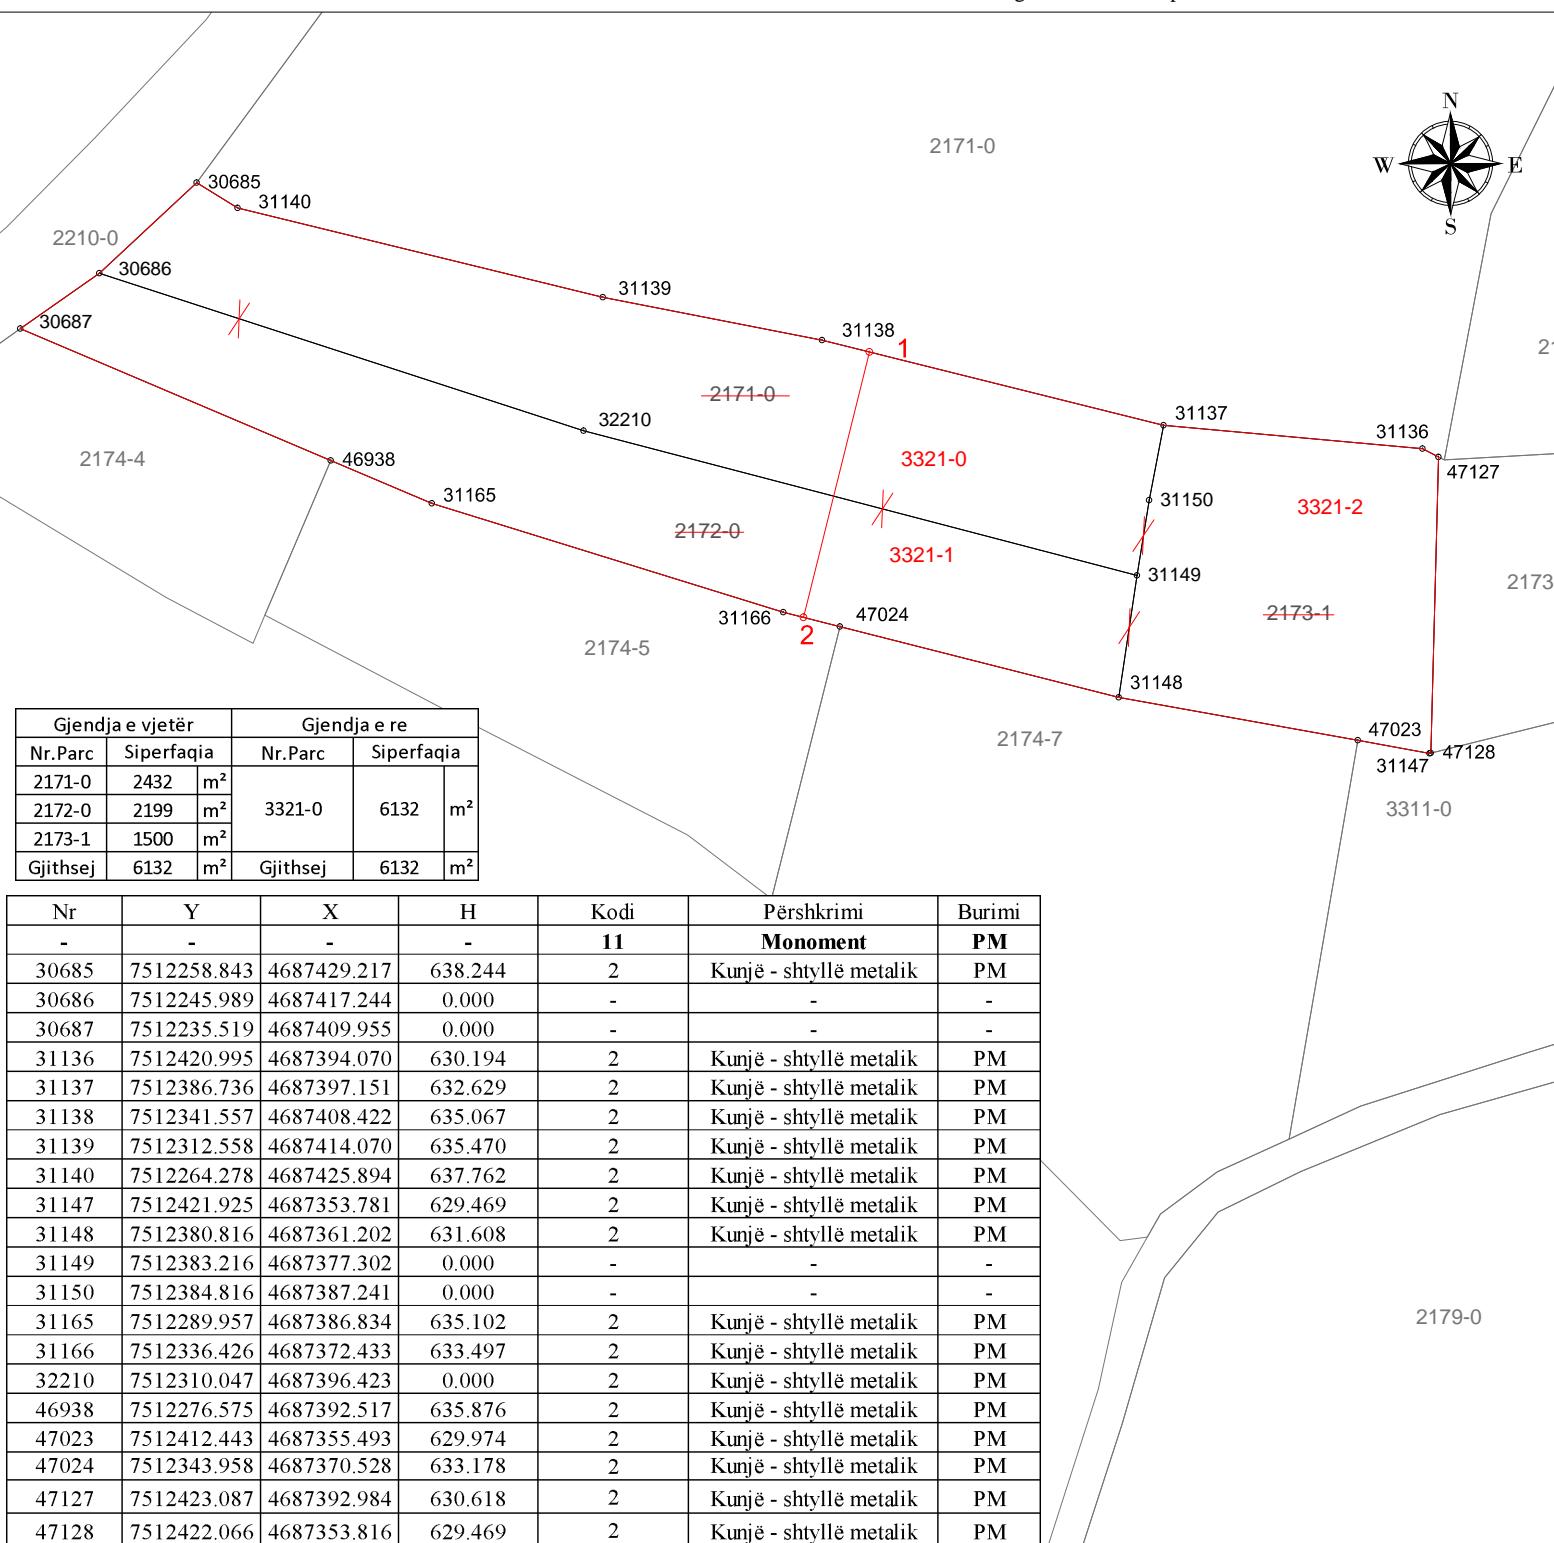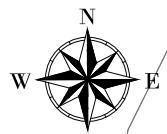

Rilevoi / Snimio: SEAD PRUSHI
(emri dhe mbiemri i gjeodetit/kompanisë/ ime i prezime geodeta/ kompanije)

Nr. i licencës / Br. licence: 152

Nënshkrimi / Potpis: _____

Data e rilevimit / Datum snimanja: 30.10.2020

Aprovoi / Usvojio: _____
(emri dhe mbiemri i pësonit zyrtar/ ime i prezime sluzbenog lica)

V.V.

Nënshkrimi / Potpis: _____

Data e aprovimit / Datum usvajanja: _____

47127,7512423.087,4687392.984,0.000,,0.000,0.000,01:00:00,1970-01-01,0.000,0.000
47128,7512422.066,4687353.816,0.000,,0.000,0.000,01:00:00,1970-01-01,0.000,0.000
47049_stk,7512356.955,4687195.600,623.439,|47049,0.159,0.167,11:36:47,2001-03-16,4.395,0.00047049
47048_stk,7512359.744,4687195.327,623.560,|47048,0.095,0.115,11:38:02,2001-03-16,3.193,0.00047048
47047_stk,7512370.402,4687194.950,624.957,|47047,0.022,0.039,11:39:12,2001-03-16,1.011,0.00047047
47046_stk,7512377.000,4687194.748,623.818,|47046,0.020,0.037,11:40:11,2001-03-16,1.009,0.00047046
32116_stk,7512385.255,4687195.277,623.592,|32116,0.126,0.149,11:41:31,2001-03-16,6.023,0.00032116
100,7512396.176,4687195.197,623.029,,0.029,0.048,11:42:45,2001-03-16,0.974,0.000
32117_stk,7512430.808,4687198.665,621.369,|32117,0.029,0.046,11:43:58,2001-03-16,0.971,0.00032117
A32117,7512430.932,4687197.527,621.325,,0.015,0.026,11:45:01,2001-03-16,0.969,0.000
32118_stk,7512460.031,4687200.301,620.035,|32118,0.011,0.018,11:46:25,2001-03-16,0.902,0.00032118
32119_stk,7512487.789,4687204.271,618.822,|32119,0.013,0.022,11:48:05,2001-03-16,0.901,0.00032119
32120_stk,7512512.005,4687209.392,617.793,|32120,0.015,0.026,11:49:13,2001-03-16,0.900,0.00032120
47045_stk,7512519.167,4687211.351,617.524,|47045,0.026,0.043,11:50:43,2001-03-16,0.822,0.00047045
A47045,7512519.244,4687210.742,617.520,,0.017,0.030,11:51:30,2001-03-16,0.821,0.000
47062_stk,7512516.149,4687224.505,618.120,|47062,0.037,0.071,11:52:55,2001-03-16,1.272,0.00047062
47044_stk,7512516.080,4687224.688,618.179,|47044,0.038,0.069,11:53:27,2001-03-16,1.275,0.00047044
A32181,7512457.380,4687200.026,620.291,,0.018,0.031,13:07:06,2001-03-16,1.032,0.000
A32182,7512470.836,4687201.552,619.596,,0.020,0.038,13:07:55,2001-03-16,1.134,0.000
A32183,7512506.827,4687207.704,617.996,,0.022,0.042,13:09:35,2001-03-16,1.134,0.000
47061_stk,7512515.396,4687227.792,618.390,|47061,0.040,0.078,13:15:19,2001-03-16,1.426,0.00047061
47060_stk,7512512.549,4687240.012,618.703,|47060,0.016,0.032,13:16:20,2001-03-16,2.223,0.00047060
31203_stk,7512495.657,4687235.051,619.655,|31203,0.016,0.032,13:18:19,2001-03-16,1.101,0.00031203
31204_stk,7512474.533,4687228.930,620.588,|31204,0.025,0.030,13:20:05,2001-03-16,1.467,0.00031204
31205_stk,7512422.052,4687221.479,622.985,|31205,0.031,0.057,13:22:13,2001-03-16,0.993,0.00031205
31179_stk,7512361.419,4687217.711,624.644,|31179,0.030,0.050,13:26:11,2001-03-16,1.174,0.00031179
A31179,7512362.005,4687217.952,624.721,,0.042,0.067,13:26:38,2001-03-16,1.018,0.000
31180_stk,7512359.483,4687204.643,624.119,|31180,0.018,0.035,13:28:01,2001-03-16,0.809,0.00031180
32116_stk1,7512385.257,4687195.309,623.395,|32116,0.034,0.053,13:29:19,2001-03-16,1.143,0.00032116
32117_stk1,7512430.847,4687198.682,621.397,|32117,0.017,0.035,13:30:48,2001-03-16,0.694,0.00032117
32118_stk1,7512460.021,4687200.311,620.081,|32118,0.018,0.036,13:31:25,2001-03-16,0.817,0.00032118
47128_stk,7512422.131,4687353.717,629.407,|47128,0.014,0.039,13:39:26,2001-03-16,1.779,0.00047128
31147_stk,7512421.966,4687353.735,629.469,|31147,0.024,0.071,13:40:37,2001-03-16,1.757,0.00031147
47127_stk,7512423.074,4687392.937,630.618,|47127,0.012,0.025,13:43:02,2001-03-16,0.702,0.00047127
31136_stk,7512420.993,4687394.032,630.194,|31136,0.015,0.027,13:44:25,2001-03-16,0.674,0.00031136
A31137,7512388.267,4687397.637,631.736,,0.014,0.029,13:46:11,2001-03-16,0.743,0.000
31137_stk,7512386.705,4687397.176,632.629,|31137,0.016,0.034,13:47:03,2001-03-16,0.822,0.00031137
1_stk,7512347.863,4687406.812,634.131,|1,0.020,0.035,13:49:17,2001-03-16,0.908,0.0001
1_2_stk,7512347.506,4687405.528,633.333,|1,0.025,0.043,13:50:43,2001-03-16,0.990,0.0001
31138_stk,7512341.712,4687408.330,635.067,|31138,0.016,0.025,13:54:15,2001-03-16,0.834,0.00031138
A31138,7512340.913,4687407.358,633.972,,0.016,0.026,13:55:05,2001-03-16,0.892,0.000
B31138,7512337.770,4687408.248,634.061,,0.013,0.021,13:56:08,2001-03-16,0.856,0.000
31139_stk,7512312.557,4687414.005,635.470,|31139,0.044,0.067,13:57:41,2001-03-16,1.337,0.00031139
31140_stk,7512264.290,4687425.889,637.762,|31140,0.028,0.041,13:59:31,2001-03-16,1.234,0.00031140
30685_stk,7512259.877,4687428.214,638.244,|30685,0.036,0.049,14:01:59,2001-03-16,1.321,0.00030685
46938_stk,7512276.539,4687392.467,635.876,|46938,0.012,0.017,14:07:26,2001-03-16,1.228,0.00046938
31165_stk,7512290.004,4687386.830,635.102,|31165,0.033,0.040,14:09:10,2001-03-16,1.828,0.00031165
31166_stk,7512336.418,4687372.426,633.497,|31166,0.036,0.041,14:10:24,2001-03-16,1.842,0.00031166
2_stk,7512339.079,4687371.738,633.397,|2,0.022,0.029,14:11:32,2001-03-16,1.584,0.0002
47024_stk,7512343.979,4687370.548,633.178,|47024,0.014,0.022,14:12:07,2001-03-16,1.411,0.00047024
31148_stk,7512380.812,4687361.168,631.608,|31148,0.022,0.031,14:13:28,2001-03-16,1.112,0.00031148
47023_stk,7512412.478,4687355.475,629.974,|47023,0.021,0.027,14:14:45,2001-03-16,1.123,0.00047023



Republika e Kosovës

Republika Kosova - Republic of Kosovo

Qeveria e Kosovës - Vlada Kosova - Government of Kosovo

Ministria e Infrastrukturës dhe Ambientit/ Ministrastvo Infrastrukture i Sredine/ Ministry of Infrastructure and Environment
AGJENCIA KADASTRALE E KOSOVËS/ KOSOVSKA KATASTARSKA AGENCIJA/ KOSOVA CADASTRAL AGENCY

GJENDJA E VJETËR / STARO STANJE											GJENDJA E RE / NOVO STANJE								
Numri rendor, Redni broj	Komuna	Opština	Zona kadastrale	Mbiemri, Emri (Emri i Babës) Adresa e vendbanimit	Nr. personal nga: Personalni Br. iz:	Nr. i Njësisë Br. Jedinice	Kultura, klasa Shfrytëzimi aktual	Përshkrimi i gjendjes së Njësisë Opis stanja Jedinice	Mbiemri, Emri (Emri i Babës) Adresa e vendbanimit	Nr. i Njësisë Br. Jedinice	Kultura, klasa Shfrytëzimi aktual	Sipërfaqja, Površina (m²)							
				Prezime, Ime (Ime Oca) Adresa prebivališta	1. Regj. i qytetarëve Registar gradana	1. (P) Parcela u/r	Aktuelna upotreba	1. Adresa, Vend i quajtur Adresa, Zvano mesto	Prezime, Ime (Ime Oca) Adresa prebivališta	1. (P) Parcels u/r	Aktuelna upotreba								
				1. Pronar - Vlasnik - Owner 2. Posedues - Posednik - Possessor 3. Shfrytëzues - Korisnik - User	2. Regj. i bizneseve Registar biznisa	2. (O) Ndërtesa u/r Zgrada		2. Infrastruktura Infrastruktura	1. Pronar - Vlasnik 2. Posedues - Posednik 3. Shfrytëzues - Korisnik	2. (O) Ndërtesa u/r Zgrada									
1	2	3	4	5	6	7	8	9	10	11	12	13	14						
1	Ferizaj	Greme	1	Tahir (Rexhep) Shehu	1	1006181216	1	2171-0 2172-0 2173-1	2432 2199 1500	Arë (5)	R	Arat e Epërmë	1	Tahir (Rexhep) Shehu	1	3321-0	R	Arë (5)	6132
																Gjithësej	6132		
Gjeodeti/kompania e licencuar: SEAD PRUSHI					Nr i licencës: 152											Nënshkrimi dhe vula:			



Republika e Kosovës
Republika Kosova-Republic of Kosovo
Qeveria e Kosovës- Vlada Kosova- Government of Kosovo
Ministria e Infrastrukturës dhe Ambientit/ Ministrastvo Infrastrukture i Sredine/ Ministry of Infrastructure and Environment
AGJENCIA KADASTRALE E KOSOVËS/KOSOVSKA KATASTARSKA AGENCIJA/ KOSOVO CADASTRAL AGENCY

Komuna: Ferizaj	Zona Kadastrale: Greme
Numri i njësisë kadastrale: 2171-0 2172-0 2173-1	Sistemi koordinat: KosovaRef01

Nr	Y	X	H	Kodi	Përvshkrimi	Burimi
-	-	-	-	11	Monoment	PM
30685	7512258.843	4687429.217	638.244	2	Kunjë - shtyllë metalik	PM
30686	7512245.989	4687417.244	0.000	-	-	-
30687	7512235.519	4687409.955	0.000	-	-	-
31136	7512420.995	4687394.070	630.194	2	Kunjë - shtyllë metalik	PM
31137	7512386.736	4687397.151	632.629	2	Kunjë - shtyllë metalik	PM
31138	7512341.557	4687408.422	635.067	2	Kunjë - shtyllë metalik	PM
31139	7512312.558	4687414.070	635.470	2	Kunjë - shtyllë metalik	PM
31140	7512264.278	4687425.894	637.762	2	Kunjë - shtyllë metalik	PM
31147	7512421.925	4687353.781	629.469	2	Kunjë - shtyllë metalik	PM
31148	7512380.816	4687361.202	631.608	2	Kunjë - shtyllë metalik	PM
31149	7512383.216	4687377.302	0.000	-	-	-
31150	7512384.816	4687387.241	0.000	-	-	-
31165	7512289.957	4687386.834	635.102	2	Kunjë - shtyllë metalik	PM
31166	7512336.426	4687372.433	633.497	2	Kunjë - shtyllë metalik	PM
32210	7512310.047	4687396.423	0.000	2	Kunjë - shtyllë metalik	PM
46938	7512276.575	4687392.517	635.876	2	Kunjë - shtyllë metalik	PM
47023	7512412.443	4687355.493	629.974	2	Kunjë - shtyllë metalik	PM
47024	7512343.958	4687370.528	633.178	2	Kunjë - shtyllë metalik	PM
47127	7512423.087	4687392.984	630.618	2	Kunjë - shtyllë metalik	PM
47128	7512422.066	4687353.816	629.469	2	Kunjë - shtyllë metalik	PM

Gjeodeti / Kompania gjeodete e licencuar:	Sead Prushi	Nënshkrimi dhe vula:	
Numri i licencës	152		



Republika e Kosovës
Republika Kosova-Republic of Kosovo
Qeveria e Kosovës- Vlada Kosova- Government of Kosovo

Ministria e Infrastrukturës dhe Ambientit/ Ministrastvo Infrastrukture i Sredine/ Ministry of Infrastructure and Environment

AGJENCIA KADASTRALE E KOSOVËS/KOSOVSKA KATASTARSKA AGENCIJA/ KOSOVO CADASTRAL AGENCY

FORMULARI PËR KORIGJIMIN E SIPËRFAQËS

Gjeodeti / Kompania gjeodete e licencuar: Sead Prushi	Numri i licencës:152
Komuna: Ferizaj	Zona Kadastrale: Greme
Numri i njësisë kadastrale: 2171-0,2172-0,2173-1	Numri i lëndës: 238/2020
Numri i njësisë kadastrale: 3321-0	

1. Tabela e ndryshimeve të sipërfaqes

Numri i parcelës	Sipërfaqja faktike (m ²)	Sipërfaqja nga SIKTK-T (m ²)	Ndryshimi (m ²)	Sipërfaqja e korrigjuar (m ²)
3321-0	6132	6092	40	6132

Bazuar në procesverbalin e terrenit, pronarët janë pajtuar me pikat definitive kufitare të vendosura në terren nga të cilat edhe është derivuar sipërfaqja definitive që regjistrohet në SIKTK.

Nënshkrimi dhe vula e gjodetit: _____

Data: _____



Republika e Kosovës
Republika Kosova-Republic of Kosovo
Qeveria e Kosovës- Vlada Kosova- Government of Kosovo

Ministria e Infrastrukturës dhe Ambientit/ Ministrastvo Infrastrukture i Sredine/ Ministry of Infrastructure and Environment

AGJENCIA KADASTRALE E KOSOVËS/KOSOVSKA KATASTARSKA AGENCIJA/ KOSOVO CADASTRAL AGENCY

RAPORTI TEKNIK

Gjeodeti / Kompania gjeodete e licencuar: Sead Prushi	Numri i licencës: 152
Komuna: Ferizaj	Zona Kadastrale: Greme
Numri i njësisë kadastrale: 2171-0,2172-0,2173-1	Lloji i lëndës: Bashkim i parcelave

Bazuar në kërkesën e palës **z. Tahir (Rexhep) Shehu** me numër personal **1006181216** të parashtruar me datën **28/10/2020**, është bërë kërkesa përmarrjen e produkteve kadastrale në Zyrën Kadastrale Komunale **Ferizaj** me datë **28/10/2020**.

Pas analizimit të dhënave me datë **30/10/2020** janë realizuar matjet në terren, përmes (**ndarjen/bashkimin**) e parcelave bazuar në (**gjendjen faktike/sipërfaqe të barazuara**).

Matjet në terren janë realizuar me instrument (GPS Leica 1230), ku fillimisht është bërë matja e pikës kontrolluese -- pastaj matjet janë realizuar bazuar në kornizën AKK nr.: 2020/01

Matje të dyfishta kontrolluese janë realizuar në pikat numër 32116,32117,32118.

Sfidat gjatë realizimit të

matjeve: _____

Matje të dyfishta kontrolluese janë realizuar në pikat numër 32116,32117,32118.

Raporti në formë tabelare:

Parcela para ndarjes/bashkimit	Sipërfaqja (m ²)	Korigjimi i sipërfaqe (po/jo)	Parcela pas ndarjes/bashkimit	Sipërfaqja (m ²)
2171-0	2432	PO	3321-0	6132
2172-0	2199			
2173-1	1500			

Nënshkrimi dhe vula e gjodetit: _____

Data: 31/10/2020



Republika e Kosovës
Republika Kosova-Republic of Kosovo
Qeveria - Vlada - Government

MINISTRIA E EKONOMISË DHE AMBIENTIT / MINISTARSTVO EKONOMIJE I ŽIVOTNE SREDINE / MINISTRY OF ECONOMY AND ENVIRONMENT
 AGJENCIA KADASTRALE E KOSOVËS / KATASTARSKA AGENCIJA KOSOVA / KOSOVO CADASTRAL AGENCY

CERTIFIKATË / CERTIFIKAT / CERTIFICATE

PERSONI / OSOBA / PERSON : SHEHU TAHIR

Numri i lëndës / Broj Predmet / Case Referent Number:	92820/2020
Data dhe koha e lëshimit / Datum i vreme izdavanja / Date and time of submission:	29.10.2020 - 09:10
Komuna / Opština / Municipality:	Ferizaj / Uroševac / Ferizaj
Zyra Kadastrale Komunale / Opštinska Katastarska Kancelarija / Municipal Cadastral Office:	Ferizaj / Uroševac / Ferizaj

A. TË DHËNAT PËR PERSONIN / PODACI O OSOBI / PERSON'S DATA

Mbiemri/Emri i afarizmit (biznesit) Prezime/ Naziv poslovanja (biznisa) Last Name / Business Name	Emri Ime First Name	Emri i babait Ime oca Father's Name	Gjinia Pol Gender	Nr. personal/biznesit Lični broj/broj poslovanja ID. No.	Shteti i shtetësisë apo regjistrimit Država državljanstva ili uknjiženja Country of citizenship	Ditëlindja/Data e themelimit Rodendan/Dan osnivanja Date of Birth/Establishmen t	Krijuar më datën Uradjeno na dan Created On	Azhuruar Ažurirano Updated
SHEHU	TAHIR	REXHEP	Mashkull / Musko / Male	KCID2203399	KOSOVA / KOSOVA / KOSOVO			

A.1 ADRESA E PERSONIT / ADRESA OSOBE / PERSON'S ADDRESS

Vendbanimi Prebivaliste Resident	Kodi Postal Poštanski Kod Postal Code	Hollësítë e adresës Pojedinosti adresë Address Details	Adresa tjetër Druga adresa Other address	Azhuruar Ažurirano Updated
GREME / GREBNO / GREME		GREBËN 132		



Zyrtari/Perqyqës / Odgovorno lice / Official person

3. NJESIA KADASTRALE/ KATASTARSKA JEDINICA/CADASTRAL UNIT

Njësie kadastrale Katastarska jedinica Cadastral unit	Komuna / Opština / Municipality	Zona kadastrale Katastarska zona Cadastral zone	Lloji i njësisë Vrsta jedinice Unit type	Tipi i pronës Tip imovine Property Type / Lloji i pronës Vrsta imovine Property kind	Kati/ Katet Br.Sprat a/ Spratova Floor number	Vendi i quajtur Zvano mesto Place name	Sipërfaqja Površina Area	Shfrytezimi aktual/Kultura- klasa Aktuelna upotreba/ Kultura-klasa Actual use/Culture-class	Pjesa e pronës Deo imovine Share quota	Lloji i së drejtës Vrsta prava Type of the right	Azhuruar /žurirano Updated
P-72217024-02172-0	Ferizaj / Uroševac / Ferizaj	GREME / GREBNO / GREME	PARCELË / PARCELA / parcel	Pronë private Privatna Imovina Privately owned Land /		ARA EPËRME / ARA EPËRME / ARA EPËRME	2171	Bujqësore - Arat - Arë E Klasës 5 // Poljoprivredno - Njive - Njiva 5 Klase // Agriculture - Arable - 5th Class Arable Land //	1 / 1	Posedim individual / Individualna Drzavina / single possessor	
P-72217024-02336-0	Ferizaj / Uroševac / Ferizaj	GREME / GREBNO / GREME	PARCELË / PARCELA / parcel	Pronë private Privatna Imovina Privately owned Land /		LAGJA E BERISHAJVE OBORR / LAGJA E BERISHAJVE OBORR / LAGJA E BERISHAJVE OBORR	549	Tokë Ndërtimore - Shtëpi-Ndërtese - / Tokë Ndërtimore - Oborr - // Gradjevinsko zemljiše - Kuca- Zgrada - / Gradjevinsko zemljiše - Dvoriše - // Construction land - House-Building - / Construction land - BackYard - //	1 / 1	Posedim individual / Individualna Drzavina / single possessor	
P-72217024-02337-0	Ferizaj / Uroševac / Ferizaj	GREME / GREBNO / GREME	PARCELË / PARCELA / parcel	Pronë private Privatna Imovina Privately owned Land /		LAGJA E BERISHAJVE TE KOPSHTI / LAGJA E BERISHAJVE TE KOPSHTI / LAGJA E BERISHAJVE TE KOPSHTI	241	Bujqësore - Arat - Arë E Klasës 3 // Poljoprivredno - Njive - Njiva 3 Klase // Agriculture - Arable - 3rd Class Arable Land //	1 / 1	Posedim individual / Individualna Drzavina / single possessor	

Zyrtari përgjegjës / Odgovorno lice / Official person

2 / 2



Republika e Kosovës
Republika Kosova-Republic of Kosovo
Qeveria - Vlada - Government

MINISTRIA E EKONOMISË DHE AMBIENTIT / MINISTARSTVO EKONOMIJE I ŽIVOTNE SREDINE / MINISTRY OF ECONOMY AND ENVIRONMENT
 AGJENCIA KADASTRALE E KOSOVËS / KATASTARSKA AGENCIJA KOSOVA / KOSOVO CADASTRAL AGENCY

CERTIFIKATË / CERTIFIKAT / CERTIFICATE

PERSONI / OSOBA / PERSON : Shehu Tahir

Numri i lëndës / Broj Predmet / Case Referent Number:	92820/2020
Data dhe koha e lëshimit / Datum i vreme izdavanja / Date and time of submission:	29.10.2020 - 09:10
Komuna / Opština / Municipality:	Ferizaj / Uroševac / Ferizaj
Zyra Kadastrale Komunale / Opštinska Katastarska Kancelarija / Municipal Cadastral Office:	Ferizaj / Uroševac / Ferizaj

A. TË DHËNAT PËR PERSONIN / PODACI O OSOBI / PERSON'S DATA

Mbiemri/Emri i afarizmit (biznesit) Prezime/ Naziv poslovanja (biznisa) Last Name / Business Name	Emri Ime First Name	Emri i babait Ime oca Father's Name	Gjinia Pol Gender	Nr. personal/biznesit Lični broj/broj poslovanja ID. No.	Shteti i shtetësisë apo regjistrimit Država državljanstva ili uknjiženja Country of citizenship	Ditëlindja/Data e themelimit Rodendan/Dan osnivanja Date of Birth/Establishmen t	Krijuar më datën Uradjeno na dan Created On	Azhuruar Ažurirano Updated
Shehu	Tahir	Rexhep	Mashkull / Musko / Male	1006181216	KOSOVA / KOSOVA / KOSOVO	15.04.1937	04.10.2019	

A.1 ADRESA E PERSONIT / ADRESA OSOBE / PERSON'S ADDRESS

Vendbanimi Prebivaliste Resident	Kodi Postal Poštanski Kod Postal Code	Hollësitë e adresës Pojedinosti adrese Address Details	Adresa tjetër Druga adresa Other address	Azhuruar Ažurirano Updated
GREME / GREBNO / GREME		Greme	Greme	

Zyrtari përgjegjës / Odgovorno lice / Official person



B. NJESIA KADASTRALE/ KATASTARSKA JEDINICA/CADASTRAL UNIT

Njësie kadastrale Katastarska jedinica Cadastral unit	Komuna / Opština / Municipality	Zona kadastrale Katastarska zona Cadastral zone	Lloji i njësisë Vrsta jedinice Unit type	Tipi i pronës Tip imovine Property Type / Lloji i pronës Vrsta imovine Property kind	Kati/ Kafet Br.Sprat a/ Spratova Floor number	Vendi i quajtur Zvano mesto Place name	Sipërfaqja Površina Area	Shfrytëzimi aktual/Kultura- klasa Aktuelna upotreba/ Kultura-klasa Actual use/Culture-class	Pjesa e pronës Deo imovine Share quota	Lloji i së drejtës Vrsta prava Type of the right	Azhuruar Ažurirano Updated
P-72217024-01411-2	Ferizaj / Uroševac / Ferizaj	GREME / GREBNO / GREME	PARCELË / PARCELA / parcel	Pronë private Privatna Imovina Privately owned Land / R		VERISHTE / VERISHTE / VERISHTE	3158	Bujqësore - Arat - Arë E Klasës 5 // Poljoprivredno - Njive - Njiva 5 Klase // Agriculture - Arable - 5th Class Arable Land //	1 / 1	Posedim individual / Individualna Drzavina / single possessor	23.10.2019
P-72217024-01411-3	Ferizaj / Uroševac / Ferizaj	GREME / GREBNO / GREME	PARCELË / PARCELA / parcel	Pronë private Privatna Imovina Privately owned Land / R		VERISHTE / VERISHTE / VERISHTE	3158	Bujqësore - Arat - Arë E Klasës 5 // Poljoprivredno - Njive - Njiva 5 Klase // Agriculture - Arable - 5th Class Arable Land //	1 / 1	Posedim individual / Individualna Drzavina / single possessor	23.10.2019
P-72217024-02171-0	Ferizaj / Uroševac / Ferizaj	GREME / GREBNO / GREME	PARCELË / PARCELA / parcel	Pronë private Privatna Imovina Privately owned Land /		ARA EPËRME / ARA EPËRME / ARA EPËRME	2421	Bujqësore - Arat - Arë E Klasës 5 // Poljoprivredno - Njive - Njiva 5 Klase // Agriculture - Arable - 5th Class Arable Land //	1 / 1	Posedim individual / Individualna Drzavina / single possessor	04.10.2019
P-72217024-02173-1	Ferizaj / Uroševac / Ferizaj	GREME / GREBNO / GREME	PARCELË / PARCELA / parcel	Pronë private Privatna Imovina Privately owned Land / R		ARA EPËRME / ARA EPËRME / ARA EPËRME	1500	Bujqësore - Arat - Arë E Klasës 5 // Poljoprivredno - Njive - Njiva 5 Klase // Agriculture - Arable - 5th Class Arable Land //	1 / 1	Posedim individual / Individualna Drzavina / single possessor	10.02.2020

