



REPUBLIKA E KOSOVËS / REPUBLIKA KOSOVA / REPUBLIC OF KOSOVO

QEVERTA E KOSOVËS / VLADA KOSOVA / GOVERNMENT OF KOSOVA

MINISTRIA E EKONOMISË DHE AMBIENTIT / MINISTARSTVO EKONOMIJE I ŽIVOTNE SREDINE / MINISTRY OF ECONOMY AND ENVIRONMENT


AGJENCIA KADASTRALE E KOSOVËS / KATASTARSKA AGENCIJA KOSOVA / KOSOVA CADASTRAL AGENCY

Rapor i njësisë kadastrale

Zonë kadastrale: Greme

Lloji i njësisë kadastrale: Parcelë

Nr i njësisë kadastrale: P-72217024-02180-0

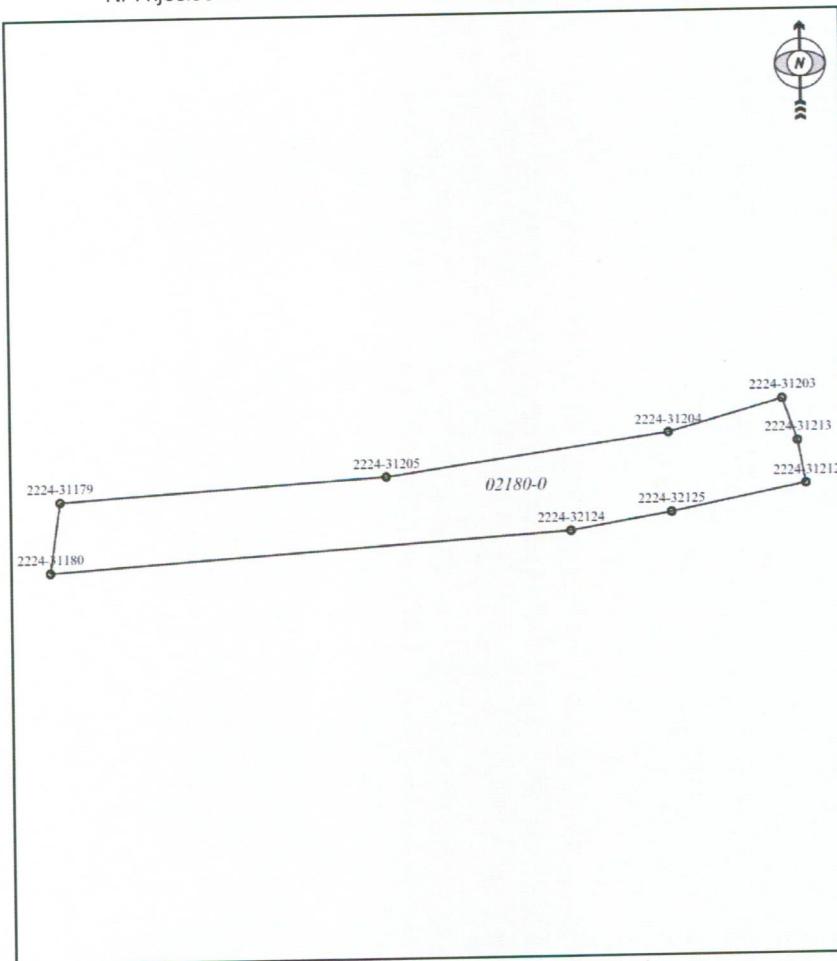

Pika	Y	X
2224-31212	7512499.911	4687219.103
2224-31215	7512474.952	4687214.094
2224-31214	7512456.222	4687210.895
2224-31180	7512359.453	4687204.618
2224-31179	7512361.413	4687217.677
2224-31205	7512422.043	4687221.445
2224-31204	7512474.532	4687228.984
2224-31203	7512495.662	4687235.043
2224-31213	7512498.431	4687227.103

S. graf. 1929.1m²

Krijuar nga

Pozita:

Emri: Fadil


Mbiemri: Ibishi

Emri i shfrytëzuesit(kodi): Fadil.Ibishi

Data 28.10.2020

Koha: 09:36:01

Nenshkrimi:

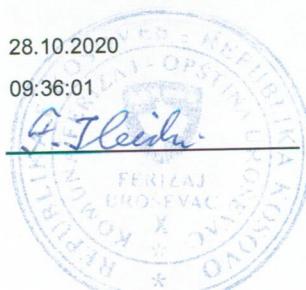



REPUBLIKA E KOSOVËS / REPUBLIKA KOSOVA / REPUBLIC OF KOSOVO
QEVERIA E KOSOVËS / VLADA KOSOVA / GOVERNMENT OF KOSOVA
MINISTRIA E EKONOMISË DHE AMBIENTIT / MINISTARSTVO EKONOMIJE I ŽIVOTNE SREDINE / MINISTRY OF ECONOMY AND ENVIRONMENT
AGJENCIA KADASTRALE E KOSOVËS / KATASTARSKA AGENCIJA KOSOVA / KOSOVA CADASTRAL AGENCY

Raport i njësisë kadastrale

Scale: 1:1288

Proceset paraprake:

Rasti	ID e Procesit	Lloji i procesit:	Data	Perdoruesi
1	597	Ngarkimi fillestari i Zonës Kadastrale	29.04.2014.	FaikK

Krijuar nga

Pozita:

Emri: Fadil


Mbiemri: Ibishi

Emri i shfrytëzuesit(kodi): Fadil.Ibishi

Data 28.10.2020

Koha: 09:36:01

Nenshkrimi:

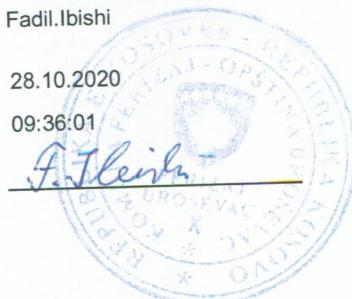



REPUBLIKA E KOSOVËS / REPUBLIKA KOSOVA / REPUBLIC OF KOSOVO

QEVERIA E KOSOVËS / VLADA KOSOVA / GOVERNMENT OF KOSOVA

MINISTRIA E EKONOMISË DHE AMBIENTIT / MINISTARSTVO EKONOMIJE I ŽIVOTNE SREDINE / MINISTRY OF ECONOMY AND ENVIRONMENT


AGJENCIA KADASTRALE E KOSOVËS / KATASTARSKA AGENCIJA KOSOVA / KOSOVA CADASTRAL AGENCY

Raport i njësisë kadastrale

Zonë kadastrale: Greme

Lloji i njësisë kadastrale: Parcelë

Nr i njësisë kadastrale: P-72217024-02181-1

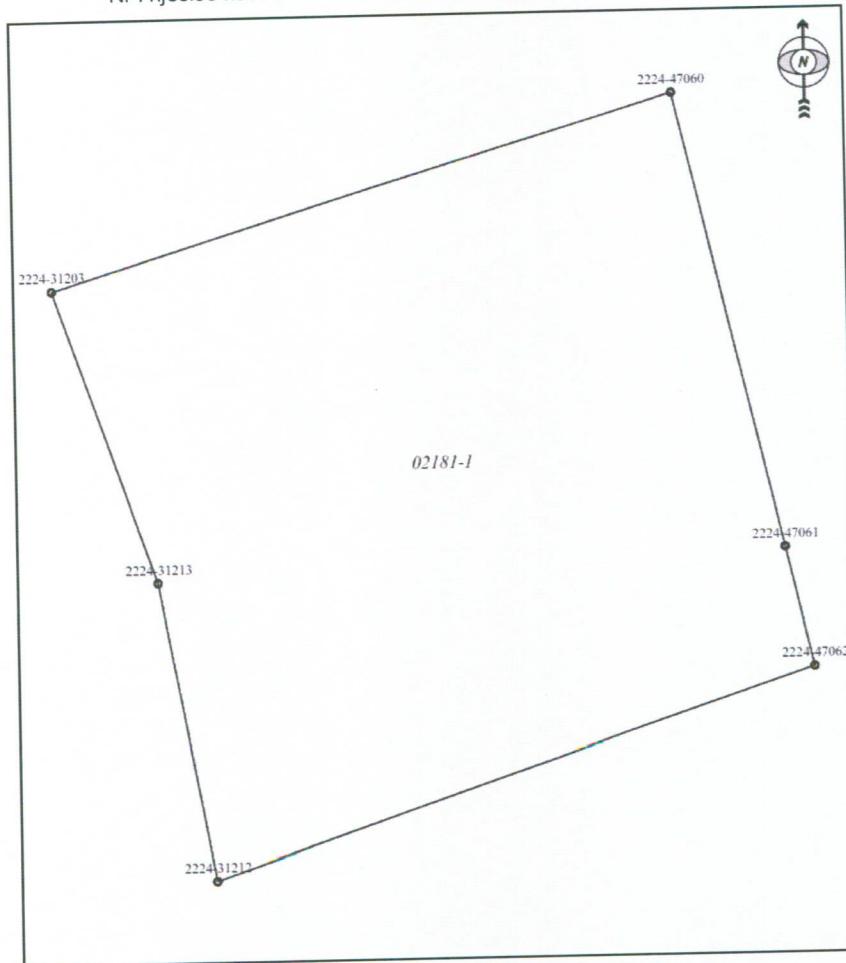

Pika	Y	X
2224-47060	7512512.546	4687240.076
2224-47061	7512515.427	4687227.764
2224-47062	7512516.171	4687224.552
2224-31212	7512499.911	4687219.103
2224-31213	7512498.431	4687227.103
2224-31203	7512495.662	4687235.043

S. graf. 276.2m²

Krijuar nga

Pozita:

Emri: Fadil


Mbiemri: Ibishi

Emri i shfrytëzuesit(kodi): Fadil.Ibishi

Data 28.10.2020

Koha: 09:37:57

Nenshkrimi:

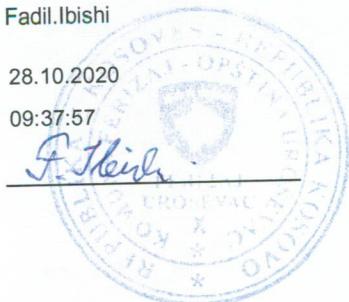



REPUBLIKA E KOSOVËS / REPUBLIKA KOSOVA / REPUBLIC OF KOSOVO

QEVERIA E KOSOVËS / VLADA KOSOVA / GOVERNMENT OF KOSOVA

MINISTRIA E EKONOMISË DHE AMBIENTIT / MINISTARSTVO EKONOMIJE I ŽIVOTNE SREDINE / MINISTRY OF ECONOMY AND ENVIRONMENT

AGJENCIA KADASTRALE E KOSOVËS / KATASTARSKA AGENCIJA KOSOVA / KOSOVA CADASTRAL AGENCY

Raport i njësisë kadastrale

Scale: 1:188

Proceset paraprake:

Rasti	ID e Procesit	Lloji i procesit:	Data	Perdoruesi
140816-2019	234970	Editimi i Parcelave dhe objekteve përkatëse të parcelës	27.11.2019.	Faton.Bislimi

Krijuar nga

Pozita:

Emri: Fadil

Mbiemri: Ibishi

Emri i shfrytëzuesit(kodi): Fadil.Ibishi

Data: 28.10.2020

Koha: 09:37:57

Nenshkrimi:





REPUBLIKA E KOSOVËS / REPUBLIKA KOSOVA / REPUBLIC OF KOSOVO


QEVERIA E KOSOVËS / VLADA KOSOVA / GOVERNMENT OF KOSOVA

MINISTRIA E EKONOMISË DHE AMBIENTIT / MINISTARSTVO EKONOMIJE I ŽIVOTNE SREDINE / MINISTRY OF ECONOMY AND ENVIRONMENT

AGJENCIA KADASTRALE E KOSOVËS / KATASTARSKA AGENCIJA KOSOVA / KOSOVA CADASTRAL AGENCY

Raport i njësisë kadastrale

Zonë kadastrale: Greme
Lloji i njësisë kadastrale: Parcelë
Nr i njësisë kadastrale: P-72217024-02183-6

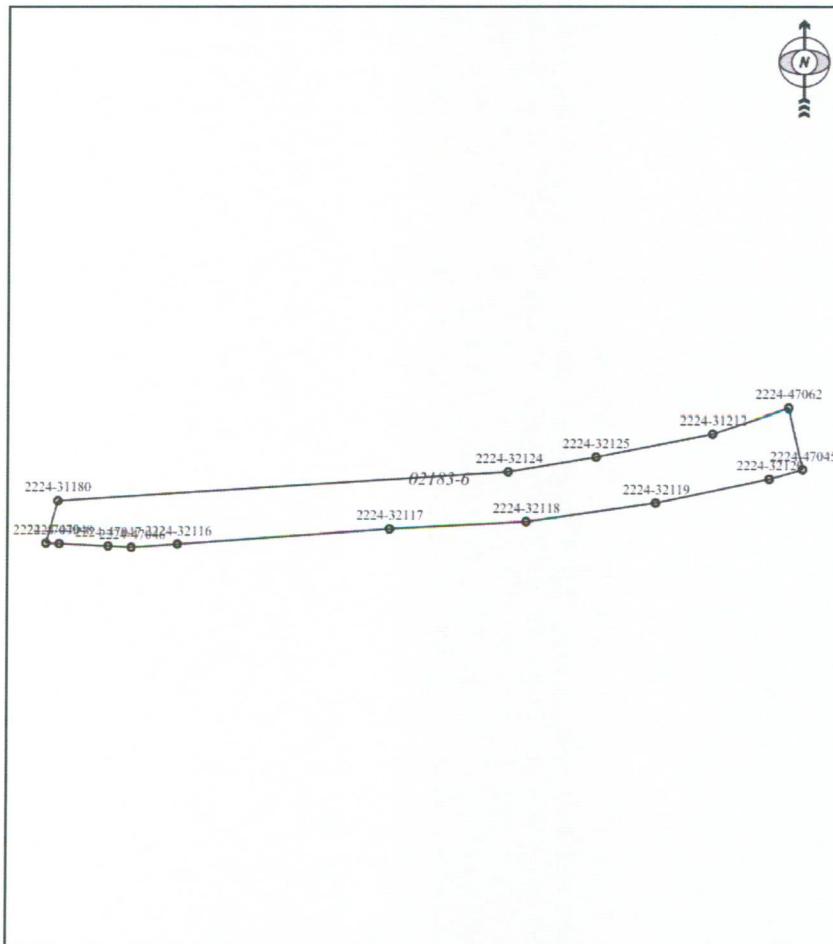

Pika	Y	X
2224-47062	7512516.171	4687224.552
2224-47045	7512519.209	4687211.437
2224-32120	7512512.041	4687209.393
2224-32119	7512487.741	4687204.274
2224-32118	7512460.052	4687200.285
2224-32117	7512430.812	4687198.686
2224-32116	7512385.273	4687195.367
2224-47046	7512375.361	4687194.667
2224-47047	7512370.343	4687194.945
2224-47048	7512359.748	4687195.459
2224-47049	7512356.905	4687195.565
2224-31180	7512359.453	4687204.618
2224-32124	7512456.222	4687210.895
2224-32125	7512474.952	4687214.094
2224-31212	7512499.911	4687219.103

Krijuar nga

Pozita:

Emri: Fadil

Mbiemri: Ibishi

Emri i shfrytëzuesit(kodi): Fadil.Ibishi

Data 28.10.2020

Koha: 09:39:27

Nenshkrimi:





REPUBLIKA E KOSOVËS / REPUBLIKA KOSOVA / REPUBLIC OF KOSOVO

QEVERTA E KOSOVËS / VLADA KOSOVA / GOVERNMENT OF KOSOVA

MINISTRIA E EKONOMISË DHE AMBIENTIT / MINISTARSTVO EKONOMIJE I ŽIVOTNE SREDINE / MINISTRY OF ECONOMY AND ENVIRONMENT

AGJENCIA KADASTRALE E KOSOVËS / KATASTARSKA AGENCIJA KOSOVA / KOSOVA CADASTRAL AGENCY

Rapor i njësisë kadastrale

Scale: 1:1488

Proceset paraprake:

Rasti	ID e Procesit	Lloji i procesit:	Data	Perdoruesi
140815/19	234631	Editimi i Parcelave dhe objekteve përkatëse të parcelës	26.11.2019.	Fadil.Ibishi

Krijuar nga

Pozita:

Emri: Fadil

Mbiemri: Ibishi

Emri i shfrytëzuesit(kodi): Fadil.Ibishi

Data: 28.10.2020

Koha: 09:39:27

Nenshkrimi:





Numri i Protokollit

239/2020

Republika e Kosovës
Republika Kosova-Republic of Kosova
Qeveria -Vlada-Government

Ministria e Mjedisit dhe Planifikimit Hapësinor /Ministarstvo Sredine i Prostornog Planiranja/Ministry of Environment and Spatial Planning
AGJENCIJA KADASTRALE E KOSOVËS/ KATASTARSKA AGECA KOSOVA/ KOSOVA CADASTRAL AGENCY

Formulari nr. 5

KËRKESË PËR SHERBIMET KADASTRALE NGA GJEODETI APO KOMPANIA GJEODETE E LICENCUAR

Gjeodeti Kompania gjeodete e licencuar: Sead Prushi

Numri i licencës: 152

Komuna: Ferizaj

Zona Kadsatrale: GREME

Numri i njësisë kadastrale: 2180-0 ,2181-1,2183-6

1. Të dhënat për parashtruesin e kërkesës

Emri / Emri i Kompanisë: Islam	Mbiemri: Shehu	Emri i prindit: Tahir
Numri personal: 1231551146	Adresa: Fsh. Greme- Ferizaj	
Numri i biznesit: (për person juridik dhe kompani)		Nr. Tel: +383 44/496-873

2. Parashtruesi i kërkesës: Pronar - Shfrytëzues - Përfaqësues i Autorizuar

3. Lista e dokumenteve të nevojshme:

Pronari/Shfrytëzuesi	Përfaqësues i Autorizuar
<input checked="" type="checkbox"/> Letërnjoftimin / Certifikatë biznesi (kopje)	<input type="checkbox"/> Letërnjoftimin / Certifikatë biznesi (kopje)
<input checked="" type="checkbox"/> Vërtetimi i tatimit në pronë	<input type="checkbox"/> Vërtetimi i tatimit në pronë
<input checked="" type="checkbox"/> Çertifikata e pronës	<input type="checkbox"/> Çertifikata e pronës
<input type="checkbox"/> Kopja e planit	<input type="checkbox"/> Kopja e planit

4. Kërkesa për:

<input type="checkbox"/> Ndërrim të kulturës së parcelës	<input type="checkbox"/> Matjen dhe regjistrimin e ndërtesës
<input type="checkbox"/> Ndarjen e parcelës	<input type="checkbox"/> Matjen dhe regjistrimin e pjesës së ndërtesës
<input checked="" type="checkbox"/> Bashkimin e parcelës	<input type="checkbox"/> Punë të veçanta gjeodezike
<input type="checkbox"/> Përcaktimin e kufijve të parcelës	<input type="checkbox"/> Matja e ndërtesës për legalizim
<input type="checkbox"/> Ri-regullimin e kuqirrit të parcelës	<input type="checkbox"/> Riregjistrim i pjesës grafike

Data: 28.10.2020

Nënshkrimi: _____





REPUBLIKA E KOSOVËS - REPUBLIKA KOSOVA - REPUBLIC OF KOSOVA
KOMUNA FERIZAJ - OPŠTINA UROŠEVAC - MUNICIPALITY OF FERIZAJ
DREJTORIA E PRONËS, KADASTRIT DHE GJEODEZISË



FATURE-RACUN-INVOICE

Nr. Serik/ Ser Br./ Ser No
2520002799

NF/FN/NB600629804

Emri/Mbiemri
Ilme/Prezime
Name/Surname

Sead Prushi

Pershkrimi
Opis
Description

**10-942/05-0091954/20 - Kërkes për blerjen e produkteve
kadastrale pikat detale 2180-0, 2181-1, 2183-**

Shuma
Iznos
Amount

22.00

Data
Datum
Date

27/10/2020

Llogaria Bankare
Broj Ziroracuna
Bank Account

1000650030000035

Nenshkrimi dhe vula e bankes
Potpis i pecat banke
Bank signature and stamp

Leshuar nga
Izdato od
Issued by

Arbenita.A.Hasani



FEG9D25200027994



I.F.J.B. VLLESACO

FLETËPAGESË

VL00281603785245

27.10.2020

028 FERIZAJ - F. BISLIMI

08:54

SHUMA:

22.00 €

PROVIZIONI:

0.80 €

TOTALI:

22.80 €

vllesapagesa

Llogaria: KOMUNA FERIZAJ

Nr. llogarisë: 1000650030000035

PAGUESI:

SEAD PRUSHI

NR.SERIK:


2520002799

PERSHKRIMI:

KERKESE PER BLERJEN

UNIREF:

FEG9D25200027994

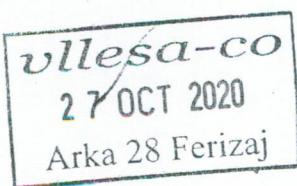

Nënshkrimi i paguesit

Nënshkrimi i arkëtarit



Matje Gjeodezike
Shërbime Kadastrale
Projektive Inxhinierike
Tel: +383 (0) 49-535-250
liridonsejdiu88@gmail.com

N.SH."Geo Coding"

Faturë

Nr: 69/2020

Shitësi:

N.SH."Goe Coding"

Blerësi:

Islam (Tahir) Shehu

Pronari:	LIRIDON SEJDIU
NRB:	811384528
mri Fiskal:	811384528
Adresa:	Rr. "12 Qershori" - Ferizaj
/Bankare	BPB - 13-04-0010027832.69
	130400100278326000.00%

Nr. ID: 1231551146
NRB:
Nr. Fiskal:
Adresa:
LL/Bankare

Data: 11/02/2020

Pagesa: Permes banks

Komenti: 1. BPB 13-04-0010027832.69
2. Banka Ekonomike 1304001002783269

Pranoi:



Doréen



Republika e Kosovës

Republika Kosova - Republic of Kosovo

Qeveria e Kosovës - Vlada Kosova - Government of Kosovo

Ministria e Infrastrukturës dhe Ambientit/ Ministrastvo Infrastrukture i Sredine/ Ministry of Infrastructure and Environment

AGJENCIA KADASTRALE E KOSOVËS/ KOSOVSKA KATASTARSKA AGENCIJA/ KOSOVA CADASTRAL AGENCY

MBËSHTJELLËS I LËNDËS

Gjeodeti / Kompania gjeodete e licencuar: **SEAD PRUSHI**

Numri i licencës: **152**

Numri i Protokollit: **239/2020**

LËNDA:

1. Ndërrim të kulturës së parcelës
2. Ndarjen e parcelës
3. Bashkimin e parcelës
4. Përcaktimin e kufijve të parcelës
5. Ri-rregullimin e kufirit të parcelës
6. Matjen dhe regjistrimin e ndërtesës
7. Matjen dhe regjistrimin e pjesës së ndërtesës
8. Regjistrimi i servitutit
9. Punë të veçanta gjeodezike
10. Matja e ndërtesës për legalizim

“GJEODET I LICENCUAR”

+383 44 791 828

e-mail: progeo2017@gmail.com

Data: **31/10/2020**

Vendi: **FERIZAJ**

.....

(Nënshkrimi dhe vula)

Përbajtja:

1. Kërkesa e palës
 2. Dëshmia e burimit të të dhënave zyrtare
 3. Dëshmia e pagesës për të dhënat e pranuara
 4. Fatura apo kuponi fiskal e lëshuar shërbimet kadastrale sipas UA 11/2019 dhe 12/2019
 5. Procesverbali nga terreni
 6. Manuali i njësive kadastrale
 7. Regjistri i ndërrimeve
 8. Lista e koordinatave të matura
 9. Formulari i korrigjimit të sipërfaqes
 10. Leternjoftimi i pronarit
 11. Certifikatën e pronësisë
 12. Raporti teknik
 13. Leternjoftimi kopje i fqinjëve
 14. Dokumentacioni i gjeodetit të licencuar

Dokumente tjerar:

BUNDESREPUBLIK DEUTSCHLAND
FEDERAL REPUBLIC OF GERMANY / REPUBLIQUE FEDERALE D'ALLEMAGNE
PERSONALAUSWEIS
IDENTITY CARD / CARTE D'IDENTITE

L77754P58

Name/ Surname-Nom

SHEHU

Vorname/Given name/Prenom

ISLAM

Geburtsstag/Date of birth/
Date de naissance

Staatsangehörigkeit/Nationality/
Nationalité

10.04.1967 DEUTSCH

Geburtsort/Place of birth/Lieu de naissance

GREME


Gültig bis/Date of expiry/
Date d'expiration

05.12.2026

294510

Unterschrift der Inhaberin/des Inhaber
Signature of bearer - Signature de la titulaire du titulaire

Shehu

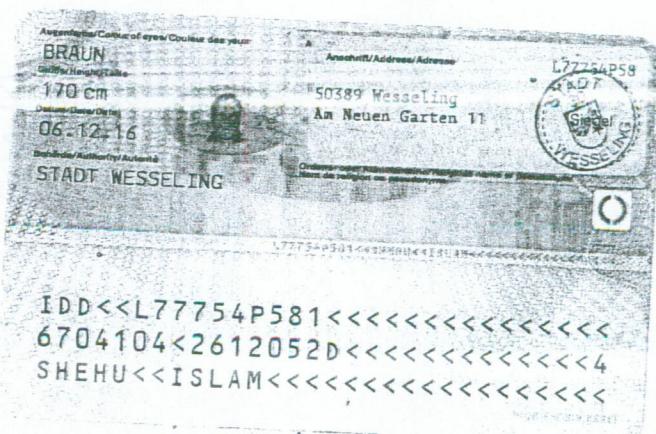



Republika e Kosovës / Republika Kosova / Republic of
Komuna e FERIZAJ / Opština UROŠEVAC / Municipality



Bazuar në nenin 18 të ligjit 03/L-204 për tatimin në pronë, si dhe udhëzimit administrativ nr. 7/2011 të lëshuar nga MF, i cili ka të bëjë me urdhëresat e ndalimit të shërbimeve komunale për detyrim të pagesës së tatimit në

Na osnovu člana 18, zakona 03/L-204 za poreza na imovinu i administrativne uredbe MF br. 7/2011, u vezi zabrane opštinskih usluga za prinudu uplate poreza na imovinu, izdaje se ova:

Based on the article 18 of LAW 03/L-204 on property tax and administrative instruction MF no. 7/2011 on termination of services for enforcement of the municipal property tax, the municipal Property Tax Office

Nr / Br / No

22529948

07/10/2020

VËRTETIM POTVRDA CERTIFICATE

Me të cilin vërtetohet se tatimpaguesi
Kojim se potvrđuje da je poreznik
that certifies that taxpayer

ISLAM SHEHU

FERIZAJ
Komuna / Opština / Municipality

FERIZAJ DËSHMORËT E KOMBIT 20
adresa / address

I ka kryer pjesërisht / plotësisht obligimet e tatimit në pronë
Delimično/ izveršio uplatu poreskih obaveza
has partially / fulfilled obligations on property tax

ISLAM TAHIR SHEHU

Vërtetimi lëshohet në bazë të kërkesës së / Potvrda se izdaje na zahtev / Certificate is issued by

Për nevoja personale
dhe shërben për / i služi za / and is used for

Shënime shtesë / Druge podatke / Aditonal info



Nenshkrimi / Potpis / Signature



Republika e Kosovës

Republika Kosova-Republic of Kosovo

Qeveria e Kosovës- Vlada Kosova- Government of Kosovo

Ministria e Infrastrukturës dhe Ambientit/ Ministrastvo Infrastrukture i Sredine/ Ministry of Infrastructure and Environment

AGJENCIA KADASTRALE E KOSOVËS/KOSOVSKA KATASTARSKA AGENCIJA/ KOSOVO CADASTRAL AGENCY

PROCESVERBALI NGA TERRENI

Gjeodeti / Kompania gjeodete e licencuar: Sead Prushi	Numri i licencës: 152
---	-----------------------

Komuna: Ferizaj	Zona Kadastrale: Greme
-----------------	------------------------

Numri i njësisë kadastrale: 2180-012183-6, 2181-1

Matja/piketimi është realizuar me:
GPS/GNSS <input checked="" type="checkbox"/>
Stacion Total <input type="checkbox"/>

1. Përshkimi i procesit:

MATJE PËR BASHKIMIN E PARCELAUE, NU Ë' PREZENT TË PALEVS TË POSHTËSHENUAR.

2. Vërejtje:

3. Nënshkrimi i palëve

Pronarët janë pajtuar me pikat definitive kufitare të vendosura në terren nga të cilat derivohet sipërfaqja definitive që do të registrohet në Sistemin e Informacioneve Kadastrale për Tokën në Kosovë.

Të poshtëshenuarve u lexohet procesverbal i dhe nëse pajtohen me atë nënshkruajnë më poshtë, në të kundërtën jepin arsyet e mospajtimit.

Emri (emri i prindit) mbiemri	Numri personal	Numri i njësisë kadastrale	Nënshkrimi
TAHIR (REXHEPI) SHENO	1006181216		Tahir Sheno

Nënshkrimi dhe vula e gjodetit:



Data: 30/10/2020



Republika e Kosovës

Republika Kosova-Republic of Kosova Qeveria -Vlada-Government

Ministria e Mjedisit dhe Planifikimit Hapësinor /Ministarstvo Sredine i Prostornog Planiranja/Ministry of Environment and Spatial Planning
AGJENCIJA KADASTRALE E KOSOVËS/ KATASTARSKA AGENCIJA KOSOVA/ KOSOVA CADASTRAL AGENCY

AGJENCIJA KADASTRALE E KOSOVËS / KATASTARSKA AGEĆIJA KOSOVA / KOSOVA CADASTRAL AGENCY

2181-1 2180-0
2183-6

Zyra kadastrale komunale / Opštinska katastarska kancelarija: Ferizaj

Z103-0

Nr. i njësisë kadastrale / Br. katastarske jedinice : _____
 Numri i lëndës / Broj predmeta:

Zona kadastrale / Katastarska zona: _____ Greme


Numri i lëndës / Broj predmeta: _____

Lloji i njësisë kadastrale / Vrsta katastarske jedinice : Parcelë

Shkalla e zvoglimit / Razmera plana : 1:1000

1 / 1

Journal of Oral Rehabilitation 2013; 40(12): 937-944

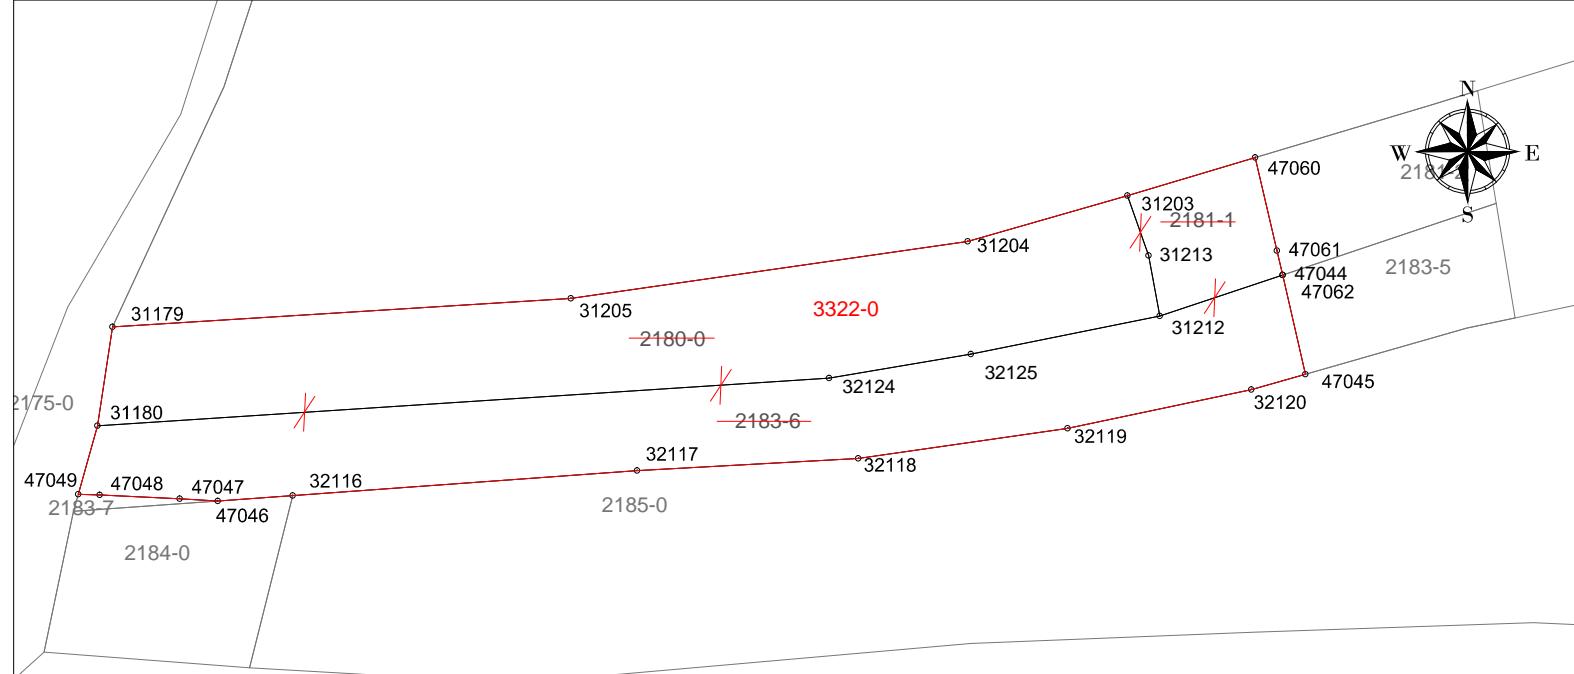

Nr	Y	X	H	Kodi	Përshkrimi	Burimi
-	-	-	-	11	Monomet	PM
31179	7512361.413	4687217.677	624.644	2	Kunjë - shtyllë metalik	PM
31180	7512359.453	4687204.618	624.119	2	Kunjë - shtyllë metalik	PM
31203	7512495.662	4687235.043	619.655	2	Kunjë - shtyllë metalik	PM
31204	7512474.532	4687228.984	620.588	2	Kunjë - shtyllë metalik	PM
31205	7512422.043	4687221.445	622.985	2	Kunjë - shtyllë metalik	PM
31212	7512499.911	4687219.103	0.000	-	-	-
31213	7512498.431	4687227.103	0.000	-	-	-
32116	7512385.273	4687195.367	623.494	2	Kunjë - shtyllë metalik	PM
32117	7512430.812	4687198.686	621.383	2	Kunjë - shtyllë metalik	PM
32118	7512460.052	4687200.285	620.058	2	Kunjë - shtyllë metalik	PM
32119	7512487.741	4687204.274	618.822	2	Kunjë - shtyllë metalik	PM
32120	7512512.041	4687209.393	617.793	2	Kunjë - shtyllë metalik	PM
32124	7512456.222	4687210.895	0.000	-	-	-
32125	7512474.952	4687214.094	0.000	-	-	-
47044	7512516.171	4687224.552	0.000	-	-	-
47045	7512519.209	4687211.437	617.524	2	Kunjë - shtyllë metalik	PM
47046	7512375.361	4687194.667	623.818	2	Kunjë - shtyllë metalik	PM
47047	7512370.343	4687194.945	624.957	2	Kunjë - shtyllë metalik	PM
47048	7512359.748	4687195.459	623.560	2	Kunjë - shtyllë metalik	PM
47049	7512356.905	4687195.565	623.439	2	Kunjë - shtyllë metalik	PM
47060	7512512.546	4687240.076	618.703	2	Kunjë - shtyllë metalik	PM
47061	7512515.427	4687227.764	618.390	2	Kunjë - shtyllë metalik	PM
47062	7512516.171	4687224.552	618.120	2	Kunjë - shtyllë metalik	PM

Gjendja e vjetër			Gjendja e re		
Nr.Parc	Siperfaqia		Nr.Parc	Siperfaqia	
2180-0	1929	m ²			
2181-1	276	m ²	3322-0	4000	m ²
2183-6	1794	m ²			
Gjithsej	4000	m ²	Gjithsej	4000	m ²

Rilevoi / Snimio: **SEAD PRUSHI**
(emri dhe mbiemri i gjeddetit/kompanisë/ ime i prezime geodeta/ kompanije)

Aprovoi / Usvojio: _____
(emri dhe mbiemri i përsonit zyrtar/ ime i prezime sluzbenog lica)

Nr. i licencës / Br. licence: 152

V V

Nënshkrimi / Potpis:

Nënshtkrimi / Potpis:

Nenškrinn / Potpis: _____

Date a rilevimit / Datum snimanja: 30.10.2020

Data e aproximit / Datum usvajanja:

47127,7512423.087,4687392.984,0.000,,0.000,0.000,01:00:00,1970-01-01,0.000,0.000
47128,7512422.066,4687353.816,0.000,,0.000,0.000,01:00:00,1970-01-01,0.000,0.000
47049_stk,7512356.955,4687195.600,623.439,|47049,0.159,0.167,11:36:47,2001-03-16,4.395,0.00047049
47048_stk,7512359.744,4687195.327,623.560,|47048,0.095,0.115,11:38:02,2001-03-16,3.193,0.00047048
47047_stk,7512370.402,4687194.950,624.957,|47047,0.022,0.039,11:39:12,2001-03-16,1.011,0.00047047
47046_stk,7512377.000,4687194.748,623.818,|47046,0.020,0.037,11:40:11,2001-03-16,1.009,0.00047046
32116_stk,7512385.255,4687195.277,623.592,|32116,0.126,0.149,11:41:31,2001-03-16,6.023,0.00032116
100,7512396.176,4687195.197,623.029,,0.029,0.048,11:42:45,2001-03-16,0.974,0.000
32117_stk,7512430.808,4687198.665,621.369,|32117,0.029,0.046,11:43:58,2001-03-16,0.971,0.00032117
A32117,7512430.932,4687197.527,621.325,,0.015,0.026,11:45:01,2001-03-16,0.969,0.000
32118_stk,7512460.031,4687200.301,620.035,|32118,0.011,0.018,11:46:25,2001-03-16,0.902,0.00032118
32119_stk,7512487.789,4687204.271,618.822,|32119,0.013,0.022,11:48:05,2001-03-16,0.901,0.00032119
32120_stk,7512512.005,4687209.392,617.793,|32120,0.015,0.026,11:49:13,2001-03-16,0.900,0.00032120
47045_stk,7512519.167,4687211.351,617.524,|47045,0.026,0.043,11:50:43,2001-03-16,0.822,0.00047045
A47045,7512519.244,4687210.742,617.520,,0.017,0.030,11:51:30,2001-03-16,0.821,0.000
47062_stk,7512516.149,4687224.505,618.120,|47062,0.037,0.071,11:52:55,2001-03-16,1.272,0.00047062
47044_stk,7512516.080,4687224.688,618.179,|47044,0.038,0.069,11:53:27,2001-03-16,1.275,0.00047044
A32181,7512457.380,4687200.026,620.291,,0.018,0.031,13:07:06,2001-03-16,1.032,0.000
A32182,7512470.836,4687201.552,619.596,,0.020,0.038,13:07:55,2001-03-16,1.134,0.000
A32183,7512506.827,4687207.704,617.996,,0.022,0.042,13:09:35,2001-03-16,1.134,0.000
47061_stk,7512515.396,4687227.792,618.390,|47061,0.040,0.078,13:15:19,2001-03-16,1.426,0.00047061
47060_stk,7512512.549,4687240.012,618.703,|47060,0.016,0.032,13:16:20,2001-03-16,2.223,0.00047060
31203_stk,7512495.657,4687235.051,619.655,|31203,0.016,0.032,13:18:19,2001-03-16,1.101,0.00031203
31204_stk,7512474.533,4687228.930,620.588,|31204,0.025,0.030,13:20:05,2001-03-16,1.467,0.00031204
31205_stk,7512422.052,4687221.479,622.985,|31205,0.031,0.057,13:22:13,2001-03-16,0.993,0.00031205
31179_stk,7512361.419,4687217.711,624.644,|31179,0.030,0.050,13:26:11,2001-03-16,1.174,0.00031179
A31179,7512362.005,4687217.952,624.721,,0.042,0.067,13:26:38,2001-03-16,1.018,0.000
31180_stk,7512359.483,4687204.643,624.119,|31180,0.018,0.035,13:28:01,2001-03-16,0.809,0.00031180
32116_stk1,7512385.257,4687195.309,623.395,|32116,0.034,0.053,13:29:19,2001-03-16,1.143,0.00032116
32117_stk1,7512430.847,4687198.682,621.397,|32117,0.017,0.035,13:30:48,2001-03-16,0.694,0.00032117
32118_stk1,7512460.021,4687200.311,620.081,|32118,0.018,0.036,13:31:25,2001-03-16,0.817,0.00032118
47128_stk,7512422.131,4687353.717,629.407,|47128,0.014,0.039,13:39:26,2001-03-16,1.779,0.00047128
31147_stk,7512421.966,4687353.735,629.469,|31147,0.024,0.071,13:40:37,2001-03-16,1.757,0.00031147
47127_stk,7512423.074,4687392.937,630.618,|47127,0.012,0.025,13:43:02,2001-03-16,0.702,0.00047127
31136_stk,7512420.993,4687394.032,630.194,|31136,0.015,0.027,13:44:25,2001-03-16,0.674,0.00031136
A31137,7512388.267,4687397.637,631.736,,0.014,0.029,13:46:11,2001-03-16,0.743,0.000
31137_stk,7512386.705,4687397.176,632.629,|31137,0.016,0.034,13:47:03,2001-03-16,0.822,0.00031137
1_stk,7512347.863,4687406.812,634.131,|1,0.020,0.035,13:49:17,2001-03-16,0.908,0.0001
1_2_stk,7512347.506,4687405.528,633.333,|1,0.025,0.043,13:50:43,2001-03-16,0.990,0.0001
31138_stk,7512341.712,4687408.330,635.067,|31138,0.016,0.025,13:54:15,2001-03-16,0.834,0.00031138
A31138,7512340.913,4687407.358,633.972,,0.016,0.026,13:55:05,2001-03-16,0.892,0.000
B31138,7512337.770,4687408.248,634.061,,0.013,0.021,13:56:08,2001-03-16,0.856,0.000
31139_stk,7512312.557,4687414.005,635.470,|31139,0.044,0.067,13:57:41,2001-03-16,1.337,0.00031139
31140_stk,7512264.290,4687425.889,637.762,|31140,0.028,0.041,13:59:31,2001-03-16,1.234,0.00031140
30685_stk,7512259.877,4687428.214,638.244,|30685,0.036,0.049,14:01:59,2001-03-16,1.321,0.00030685
46938_stk,7512276.539,4687392.467,635.876,|46938,0.012,0.017,14:07:26,2001-03-16,1.228,0.00046938
31165_stk,7512290.004,4687386.830,635.102,|31165,0.033,0.040,14:09:10,2001-03-16,1.828,0.00031165
31166_stk,7512336.418,4687372.426,633.497,|31166,0.036,0.041,14:10:24,2001-03-16,1.842,0.00031166
2_stk,7512339.079,4687371.738,633.397,|2,0.022,0.029,14:11:32,2001-03-16,1.584,0.0002
47024_stk,7512343.979,4687370.548,633.178,|47024,0.014,0.022,14:12:07,2001-03-16,1.411,0.00047024
31148_stk,7512380.812,4687361.168,631.608,|31148,0.022,0.031,14:13:28,2001-03-16,1.112,0.00031148
47023_stk,7512412.478,4687355.475,629.974,|47023,0.021,0.027,14:14:45,2001-03-16,1.123,0.00047023



Republika e Kosovës

Republika Kosova - Republic of Kosovo

Qeveria e Kosovës - Vlada Kosova - Government of Kosovo

Ministria e Infrastrukturës dhe Ambientit/ Ministrastvo Infrastrukture i Sredine/ Ministry of Infrastructure and Environment
AGJENCIA KADASTRALE E KOSOVËS/ KOSOVSKA KATASTARSKA AGENCIJA/ KOSOVA CADASTRAL AGENCY



Republika e Kosovës
Republika Kosova-Republic of Kosovo
Qeveria e Kosovës- Vlada Kosova- Government of Kosovo
Ministria e Infrastrukturës dhe Ambientit/ Ministrastvo Infrastrukture i Sredine/ Ministry of Infrastructure and Environment
AGJENCIA KADASTRALE E KOSOVËS/KOSOVSKA KATASTARSKA AGENCIJA/ KOSOVO CADASTRAL AGENCY

Komuna: Ferizaj	Zona Kadastrale: Greme
Numri i njësis kadastrale: 2181-1,2180-0,2183-6	Sistemi koordinat: KosovaRef01

Nr	Y	X	H	Kodi	Përvshkrimi	Burimi
-	-	-	-	11	Monoment	PM
31179	7512361.413	4687217.677	624.644	2	Kunjë - shtyllë metalik	PM
31180	7512359.453	4687204.618	624.119	2	Kunjë - shtyllë metalik	PM
31203	7512495.662	4687235.043	619.655	2	Kunjë - shtyllë metalik	PM
31204	7512474.552	4687228.984	620.588	2	Kunjë - shtyllë metalik	PM
31205	7512422.043	4687221.445	622.985	2	Kunjë - shtyllë metalik	PM
31212	7512499.911	4687219.103	0.000	-	-	-
31213	7512498.431	4687227.103	0.000	-	-	-
32116	7512385.273	4687195.367	623.494	2	Kunjë - shtyllë metalik	PM
32117	7512430.812	4687198.686	621.383	2	Kunjë - shtyllë metalik	PM
32118	7512460.052	4687200.285	620.058	2	Kunjë - shtyllë metalik	PM
32119	7512487.741	4687204.274	618.822	2	Kunjë - shtyllë metalik	PM
32120	7512512.041	4687209.393	617.793	2	Kunjë - shtyllë metalik	PM
32124	7512456.222	4687210.895	0.000	-	-	-
32125	7512474.952	4687214.094	0.000	-	-	-
47044	7512516.171	4687224.552	0.000	-	-	-
47045	7512519.209	4687211.437	617.524	2	Kunjë - shtyllë metalik	PM
47046	7512375.361	4687194.667	623.818	2	Kunjë - shtyllë metalik	PM
47047	7512370.343	4687194.945	624.957	2	Kunjë - shtyllë metalik	PM
47048	7512359.748	4687195.459	623.560	2	Kunjë - shtyllë metalik	PM
47049	7512356.905	4687195.565	623.439	2	Kunjë - shtyllë metalik	PM
47060	7512512.546	4687240.076	618.703	2	Kunjë - shtyllë metalik	PM
47061	7512515.427	4687227.764	618.390	2	Kunjë - shtyllë metalik	PM
47062	7512516.171	4687224.552	618.120	2	Kunjë - shtyllë metalik	PM

Matja e pikave në dy seri							
Seria	Nr. Pikës	Y	X	H	ΔY	ΔX	ΔP
I	32116	7512385.26	4687195.28	623.59	-0.0020	-0.0320	0.0321
II	32116	7512385.26	4687195.31	623.40			
I	32117	7512430.847	4687198.682	621.40			
II	32117	7512430.808	4687198.665	621.37	0.0390	0.0170	0.0425
I	32118	7512460.03	4687200.30	620.04			
II	32118	7512460.02	4687200.31	620.08			
					0.0100	-0.0100	0.0141

Koordinatat përfundimtare			
Nr	Y	X	H
32116	7512385.256	4687195.293	623.494
32117	7512430.828	4687198.674	621.383
32118	7512460.026	4687200.306	620.058

Gjeodeti / Kompania gjeodete e licencuar:	Sead Prushi	Nënshkrimi dhe vula:	
Numri i licencës	152		



Republika e Kosovës
Republika Kosova-Republic of Kosovo
Qeveria e Kosovës- Vlada Kosova- Government of Kosovo

Ministria e Infrastrukturës dhe Ambientit/ Ministrastvo Infrastrukture i Sredine/ Ministry of Infrastructure and Environment

AGJENCIA KADASTRALE E KOSOVËS/KOSOVSKA KATASTARSKA AGENCIJA/ KOSOVO CADASTRAL AGENCY

FORMULARI PËR KORIGJIMIN E SIPËRFAQËS

Gjeodeti / Kompania gjeodete e licencuar: Sead Prushi	Numri i licencës:152
Komuna: Ferizaj	Zona Kadastrale: Greme
Numri i njësisë kadastrale: 2180-0,2181-1,2183-6	Numri i lëndës: 239/2020
Numri i njësisë kadastrale: 3322-0	

1. Tabela e ndryshimeve të sipërfaqes

Numri i parcelës	Sipërfaqja faktike (m ²)	Sipërfaqja nga SIKTK-T (m ²)	Ndryshimi (m ²)	Sipërfaqja e korrigjuar (m ²)
3322-0	4000	3986	14	4000

Bazuar në procesverbalin e terrenit, pronarët janë pajtuar me pikat definitive kufitare të vendosura në terren nga të cilat edhe është derivuar sipërfaqja definitive që regjistrohet në SIKTK.

Nënshkrimi dhe vula e gjodetit: _____

Data: _____



Republika e Kosovës
Republika Kosova-Republic of Kosovo
Qeveria e Kosovës- Vlada Kosova- Government of Kosovo

Ministria e Infrastrukturës dhe Ambientit/ Ministrastvo Infrastrukture i Sredine/ Ministry of Infrastructure and Environment

AGJENCIA KADASTRALE E KOSOVËS/KOSOVSKA KATASTARSKA AGENCIJA/ KOSOVO CADASTRAL AGENCY

RAPORTI TEKNIK

Gjeodeti / Kompania gjeodete e licencuar: Sead Prushi	Numri i licencës: 152
Komuna: Ferizaj	Zona Kadastrale: Greme
Numri i njësisë kadastrale: 2180-0,2181-1,2183-6	Lloji i lëndës: Bashkim i parcelave

Bazuar në kërkesën e palës **z. Islam (Tahir) Shehu** me numër personal **1231551146** të parashtruar me datën **28/10/2020**,
është bërë kërkesa përmarrjen e produkteve kadastrale në Zyrën Kadastrale Komunale **Ferizaj** me datë **28/10/2020**.
Pas analizimit të të dhënavë me datë **30/10/2020** janë realizuar matjet në terren, përmarrjen e **bashkimin** e parcelave
bazuar në (**gjendjen faktike/sipërfaqe të barazuara**).

Matjet në terren janë realizuar me instrument (GPS Leica 1230), ku fillimisht është bërë matja e pikës kontrolluese –
pastaj matjet janë realizuar bazuar në kornizën AKK nr.: 2020/01

Matje të dyfishta kontrolluese janë realizuar në pikat numër 32116,32117,32118.

Sfidat gjatë realizimit të

matjeve: _____

Matje të dyfishta kontrolluese janë realizuar në pikat numër 32116,32117,32118.

Raporti në formë tabelare:

Parcela para ndarjes/bashkimit	Sipërfaqja (m ²)	Korigjimi i sipërfaqe (po/jo)	Parcela pas ndarjes/bashkimit	Sipërfaqja (m ²)
2180-0	1929	PO	3322-0	4000
2181-1	276			
2183-6	1794			

Nënshkrimi dhe vula e gjodetit: _____

Data: 31/10/2020



Republika e Kosovës
Republika Kosova-Republic of Kosovo
Qeveria - Vlada - Government

**MINISTRIA E EKONOMISË DHE AMBIENTIT / MINISTARSTVO EKONOMIJE I ŽIVOTNE SREDINE / MINISTRY OF ECONOMY
AND ENVIRONMENT**
AGJENCIA KADASTRALE E KOSOVËS / KATASTARSKA AGENCIJA KOSOVA / KOSOVO CADASTRAL AGENCY

Komuna: Ferizaj
Zyre: Zyrë kadastrale komunale

Numri referent i lëndës: 84294-2020

Në mbështetje të Nenit 3 të Ligjit Nr. 2002/5 mbi Themelimin e Regjistrimit të Drejtave të Pronës së Paluajtshme, Ligjet Nr. 2003/13 dhe neni 4 i Ligjit Nr. 04/L-009, në bazë të kërkesës së Islam (Tahir) Shehu, me numër personal 1231551146, nxjerr këtë:

AKTVENDIM

APROVOHET – Kërkesa e parashtruar nga Islam (Tahir) Shehu, me numër personal 1231551146, e cila ka të bëjë me Bartja e poseditim - Dhurim, sipas aktit juridik _____ në njësinë të kadastrale:

Numri kadastrale	Zona Kadastrale	Vendi i quajtur	Sipërfaqja e gjithmbarshme	Të dhënët për gjendjen e re të krijuar
P-72217024-02180-0	GREME	ARA EPËRME	1916	me 1/1 e pjeses ideale
P-72217024-02181-1	GREME	ARA EPËRME	276	me 1/1 e pjeses ideale
P-72217024-02183-6	GREME	ARA EPËRME	1794	me 1/1 e pjeses ideale

Arsyetim

Zyra Kadastrale Komunale Ferizaj ka pranuar kërkesën e parashtruar nga Islam (Tahir) Shehu, me numër personal 1231551146, për regjistrimin e të drejtave në Regjistrin e të Drejtave të Pronës së Paluajtshme dhe kërkesës së tij-saj ia ka bashkangjitur dëshmitë e plota për regjistrim (lloji i dokumentit): Kontrata për Dhurimin e Palaujtshmerise, me nr. LRP- 3627/2020, REF. NR. 1492 /2020, noteri Nexhat Qorrolli, dëshmia e pagesës se taksës nr. serik 079718, letërnjoftimi kopje dhe vërtetimi tatimit në pronë.

Sipas gjendjes së konstatuar janë plotësuar të gjitha kushtet për regjistrim sipas dispozitave të cekura më lart.

Këshilla Juridike: Pala e pakënaqur ka të drejtë që në afatin prej tridhjetë (30) ditësh, nga dita e pranimit të këtij Aktvendimi të kërkoj nga ZKK rishqyrtimin e tij.


Aktvendimi i dorëzohet:

Arkivit,
Shërbimit përkatës,
Parashtruesit të kërkesës

Zyrtari përgjegjës
Zekri Bytyci

Data: 12.10.2020

Drejtori
Sabri Murseli

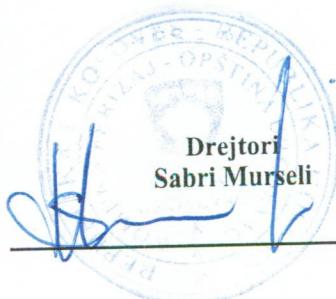



Republika e Kosovës
Republika Kosova-Republic of Kosovo
Qeveria - Vlada - Government

MINISTRIA E EKONOMISË DHE AMBIENTIT / MINISTARSTVO EKONOMIJE I ŽIVOTNE SREDINE / MINISTRY OF ECONOMY AND ENVIRONMENT
AGJENCIA KADASTRALE E KOSOVËS / KATASTARSKA AGENCIJA KOSOVA / KOSOVO CADASTRAL AGENCY

CERTIFIKATË / CERTIFIKAT / CERTIFICATE

PERSONI / OSOBA / PERSON : Shehu Islam

Numri i lëndës / Broj Predmet / Case Referent Number:	84294-2020
Data dhe koha e lëshimit / Datum i vreme izdavanja / Date and time of submission:	28.10.2020 - 08:45
Komuna / Opština / Municipality:	Ferizaj / Uroševac / Ferizaj
Zyra Kadastrale Komunale / Opštinska Katastarska Kancelarija / Municipal Cadastral Office:	Ferizaj / Uroševac / Ferizaj

A. TË DHËNAT PËR PERSONIN / PODACI O OSOBI / PERSON'S DATA

Mbiemri/Emri i afarizmit (biznesit) Prezime/ Naziv poslovanja (biznisa) Last Name / Business Name	Emri Ime First Name	Emri i babait Ime oca Father's Name	Gjinia Pol Gender	Nr. personal/ biznesit Lični broj/broj poslovanja ID. No.	Shteti i shtetësisë apo regjistrimit Država državljanstva ili uknjiženja Country of citizenship	Ditëlindja/Data e themelimit Rodendan/Dan osnivanja Date of Birth/Establishmen t	Krijuar më datën Uradjeno na dan Created On	Azhuruar Ažurirano Updated
Shehu	Islam	Tahir	Mashkull / Musko / Male	1231551146	KOSOVA / KOSOVA / KOSOVO	10.04.1967	28.10.2020	

A.1 ADRESA E PERSONIT / ADRESA OSOBE / PERSON'S ADDRESS

Vendbanimi Prebivaliste Resident	Kodi Postal Poštanski Kod Postal Code	Hollësitë e adresës Pojedinosti adrese Address Details	Adresa tjetër Druga adresa Other address	Azhuruar Ažurirano Updated
GREME / GREBNO / GREME		Greme	Greme	



B. NJESIA KADASTRALE/ KATASTARSKA JEDINICA/CADASTRAL UNIT

Njësia kadastrale Katastarska jedinica Cadastral unit	Komuna / Opština / Municipality	Zona kadastrale Katastarska zona Cadastral zone	Lloji i njësisë Vrsta jedinice Unit type	Tipi i pronës Tip imovine Property Type / Lloji i i pronës Vrsta imovine Property kind	Kati/ Katet Br.Sprat a/ Spratova Floor number	Vendi i quajtur Zvano mesto Place name	Sipërfaqja Površina Area	Shfrytezimi aktual/Kultura- klasa Aktuelna upotreba/ Kultura-klasa Actual use/Culture-class	Pjesa e pronës Deo imovine Share quota	Lloji i së drejtës Vrsta prava Type of the right
P-72217024-02180-0	Ferizaj / Uroševac / Ferizaj	GREME / GREBNO / GREME	PARCELË / PARCELA / parcel	Pronë private Privatna Imovina Privately owned Land /		ARA EPËRME / ARA EPËRME / ARA EPËRME	1916	Bujqësore - Arat - Arë E Klasës 5 // Poljoprivredno - Njive - Njiva 5 Klase / / Agriculture - Arable - 5th Class Arable Land / /	1 / 1	Posedim individual / Individualna Drzavina / single possessor
P-72217024-02181-1	Ferizaj / Uroševac / Ferizaj	GREME / GREBNO / GREME	PARCELË / PARCELA / parcel	Pronë private Privatna Imovina Privately owned Land / R		ARA EPËRME / ARA EPËRME / ARA EPËRME	276	Bujqësore - Arat - Arë E Klasës 5 // Poljoprivredno - Njive - Njiva 5 Klase / / Agriculture - Arable - 5th Class Arable Land / /	1 / 1	Posedim individual / Individualna Drzavina / single possessor
P-72217024-02183-6	Ferizaj / Uroševac / Ferizaj	GREME / GREBNO / GREME	PARCELË / PARCELA / parcel	Pronë private Privatna Imovina Privately owned Land / R		ARA EPËRME / ARA EPËRME / ARA EPËRME	1794	Bujqësore - Arat - Arë E Klasës 5 // Poljoprivredno - Njive - Njiva 5 Klase / / Agriculture - Arable - 5th Class Arable Land / /	1 / 1	Posedim individual / Individualna Drzavina / single possessor



REPUBLIKA E KOSOVËS

N O T E R
NEXHAT SH.QORROLLI
FERIZAJ

LRP.nr.3628/2020

Më: (2020-10-05) Gjashtë Tetor dymjë e njëzetë, para meje, Noter: Nexhat Qorrolli,i nënshkruar në fund me seli të zyrës noteriale në Ferizaj, rr. "Reçakut" p.n., është paraqitur:

Islam (Tahir) Shehu, i/e lindur me 10/04/1967, në Greme, zotësia e veprimit e plotë, me vendbanim në Greme K.Ferizaj, i/e identifikuar përmes letërnjoftimit me numër: L77754P58, lëshuar nga autoritetet e R.F.Gjermanisë, me vlefshmëri deri me 05.12.2026, dhe sipas certifikatës së lindjes me numër personal:1231551146, lëshuar nga Komuna, Zyra e Gjendjes Civile Ferizaj, në cilësinë: Autorizuesi, me kërkesë që ta përpiloj këtë akt notarial me sa vijon:

AUTORIZIM I PËRGJITHSHËM PËR PËRFAQËSIM

Unë: **Islam Shehu**, E AUTORIZOJË babain tim: **Tahir (Rexhep) Shehu**, i/e lindur me 15/04/1937, në Greme, zotësia e veprimit e plotë, me vendbanim në fsh.Greme K. Ferizaj, shtetas Kosovar, i/e identifikuar përmes letërnjoftimit me numër personal: 1006181216, lëshuar nga MPB-ja e RKS-së, që mund në emër timin dhe llogarinë time të më përfaqësoj në veprimët juridike në të gjitha organët administrative dhe ato gjyqësore në Republikës së Kosovës.

I autorizuari mund të më përfaqësojë pranë Zyrës kadastrale Komunale dhe të gjitha organeve komunale lidhur me bashkinin e parcelave me numër P-72217024-02180-0, P-72217024-02181-1 dhe P-72217024-02183-6, të gjitha në Z.K.Greme Ferizaj.

Ky autorizim nuk është i kufizuar në kohë.

Të gjitha veprimët juridike të cilat i ndermerr i autorizuari im i pranoj me të gjitha perjegjësit ligjore.

Pasojat ligjore të këtij autorizimi më u janë spjeguar nga Noteri dhe i pranoj me të gjitha përgjegjësitë ligjore.

Kompenzimi për përplimin e këtij akti notarial nga ana e noterit është llogaritur sipas Udhëzimit administrativ 02/2012 - neni 21 pika 8 të tarifës në lartësi prej dhjetë euro (10 euro) +TVSH-ja 18% Totali për pages: 11.80 euro.

Ky akt notarial është përpiluar në 2 (dy) ekzemplar origjinal nga të cilat 1(një) i merr dhënësi i autorizimit ndërsa 1 (një) mbetet në dosje noteriale.

Noteri palës ia levoi këtë akt notarial, ku pas pyetjes së drejtëpërdrejtë u bind se ky autorizim i cili ipet i përgjigjet vullnetit të shprehur të tij, pas së cilës pala deklaroj se e ka kuptuar në tërësi përbajtjen dhe është i pajtueshëm me të.

Dokumentet që i bashkangjitën këtij akti en brevet- dosjës së originalit: kopja e letërnjoftimit të Autorizuesit, kopja e Letërnjoftimit të të Autorizuarit.

Veprimi i noterizimit u krye pandërpre në Ferizaj, me datë 06.10.2020, në ora-10:50.

DHËNËSI I AUTORIZIMIT:Islam Shehu

Nënshkrimi:



NOTERI: Nexhat Sh. Qorrolli,